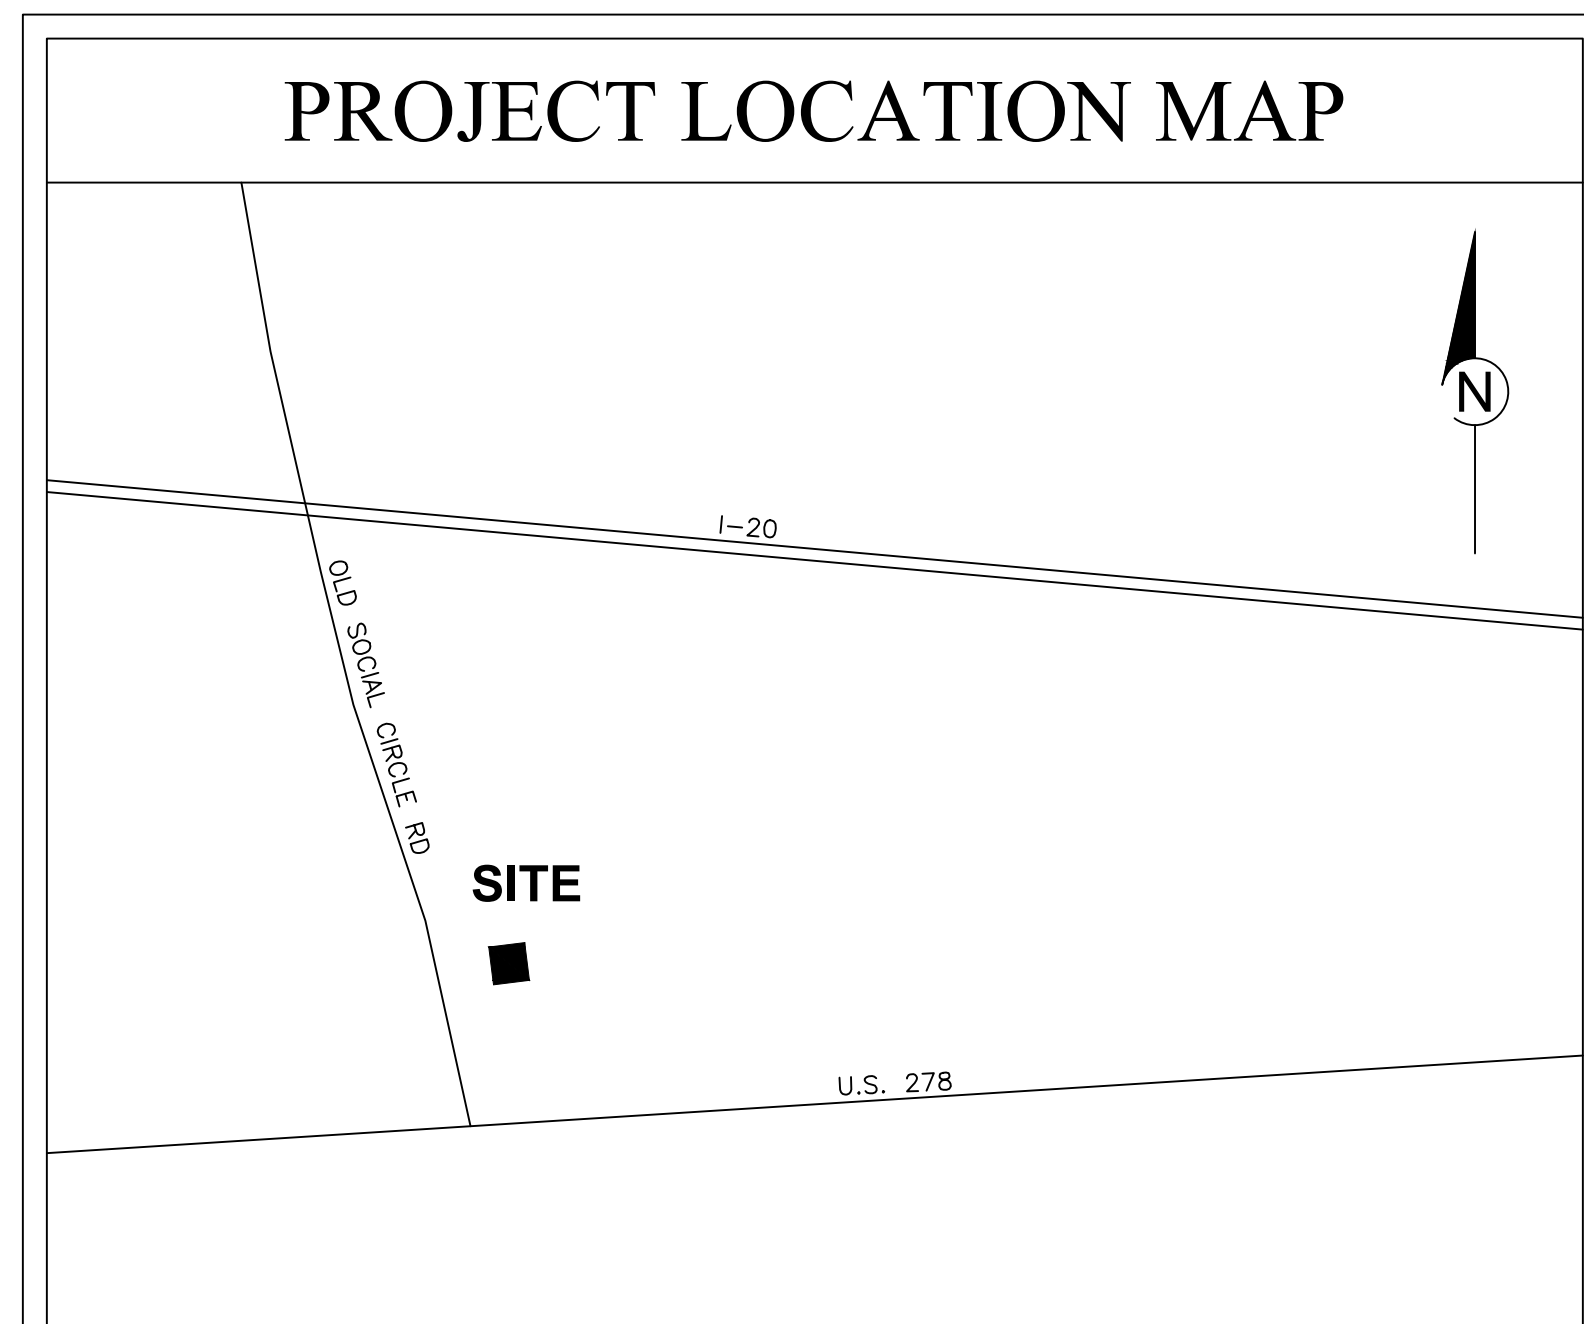


ROCK BAPTIST CHURCH
NEW FACILITY
AT
U.S. HIGHWAY 278
SOCIAL CIRCLE, GEORGIA 30025



PROJECT CRITERIA

CURRENT LIST OF CODES:

INTERNATIONAL BUILDING CODE, 2018 EDITION WITH GA AMENDMENTS
INTERNATIONAL FIRE CODE, 2018 EDITION
INTERNATIONAL PLUMBING CODE, 2018 EDITION WITH GA AMENDMENTS
INTERNATIONAL MECHANICAL CODE, 2018 EDITION WITH GA AMENDMENTS
INTERNATIONAL FUEL GAS CODE, 2018 EDITION WITH GA AMENDMENTS
NATIONAL ELECTRICAL CODE, 2020 EDITION
INTERNATIONAL ENERGY CONSERVATION CODE, 2015 EDITION WITH GA AMENDMENTS
NFPA 101 LIFE SAFETY CODE, 2018 EDITION
2010 ADA STANDARDS FOR ACCESSIBLE DESIGN

BUILDING DESIGN CRITERIA:

- Use & Occupancy Classification: LSC 101 Ch.6 (IBC Ch.3)
 - New Assembly (A-3)
- Occupant Load (LSC & IBC) (Refer to Occupancy Calculations)
 - Total: 987 persons
- Hazard Contents (LSC Section 6.2.2)
 - Low Hazard
- Special Requirements (IBC Ch. 4)
 - Platform Construction
- Type of Construction (IBC Ch.5 & 6)
 - Type II-B, Sprinkled
 - IBC Table 601 = No fire-rating requirements for structure
 - IBC Table 602 = No fire-rating requirements based on distance
- Building Area (IBC Table 506.2)
 - A-3 38,000 sf max
 - Project: 20,607 sf overall area
- Building Stories/Height
 - A-3 (3 stories, 75' max)
 - Project: Single Story, 32' highest point
- Fire sprinkler system
 - NFPA 13 Sprinkler System
- Egress Capacity
 - Refer to sheet A-1.1 for calculations and layout
- Design Loads
 - Refer to structural drawings and/or PEMB drawings

PROJECT DESCRIPTION:

New 20,607 sf single story Worship Facility formed from multiple metal building single slope systems housing a 300 seat worship area, main foyer & lobby, offices, classrooms, and warming kitchen

OCCUPANCY CALCULATIONS: (LSC Table 7.3.1.2, IBC Table 1004.1.2)

<u>Space</u>	<u>Area</u>	<u>Occupancy</u>	<u>Load</u>
Worship Area:	3,955 sf	A-3 (7 net)	565.00 persons
Platform:	1,254 sf	A-3 (15 net)	83.60 persons
Sound Booth:	146 sf	actual	3.00 persons
Recording Room:	322 sf	B (150 gross)	2.15 persons
Green Room:	296 sf	A-3 (15 net)	19.73 persons
Cry Room:	110 sf	E (20 net)	5.50 persons
Classrooms:	6,022 sf	E (20 net)	301.10 persons
Office:	358 sf	B (150 gross)	2.38 persons
Warming Kitchen:	425 sf	Kitchen (100 gross)	4.25 persons
		Total:	986.71 ~ 987 persons

PLUMBING FIXTURE CALCULATIONS:

Occupant load:
987 persons total (494 men / 494 women)

Water Closets:
 494 men / 150 = 3.29 = 4 wc required
 494 women / 75 = 6.58 = 7 wc required

Lavatories:
 $987 \text{ people} / 200 = 4.93 = 5 \text{ lavatory required}$

Drinking Fountains:
One required per 1000 occupants = $987 / 1000 = 0.987 \sim 1$ required

SHEET INDEX

SHT. No.	TITLE
CS-1	COVER SHEET
A-1	OVERALL FLOOR PLAN
A-1.1	LIFE SAFETY PLAN
A-2	RCP & SCHEDULES
A-3	EXTERIOR ELEVATIONS
A-4	BLDG. & WALL SECTIONS
A-5	ENLARGED PLANS & INTERIOR ELEVATIONS
A-6	ENLARGED PLANS & INTERIOR ELEVATIONS
A-7	SECTIONS AND DETAILS
S-1	FOUNDATION PLAN
M-1	HVAC FLOOR PLAN
M-2	HVAC DETAILS & SCHEDULES
M-3	HVAC NOTES & OA CALCULATIONS
E-1	POWER PLAN
E-2	LIGHTING PLAN
E-3	RISER AND PANEL SCHEDULES
E-4	NOTES AND LEGEND
P-1	SANITARY FLOOR PLAN
P-2	POTABLE WATER FLOOR PLAN
P-3	PLUMBING NOTES & DETAILS
P-4	PLUMBING ISOMETRICS
P-5	PLUMBING ISOMETRICS
PEMB	PRE-ENGINEERED METAL BUILDING PLANS
	FIRE SPRINKLER DRAWINGS TO BE SUBMITTED BY AWARDED CONTRACTOR
	FIRE ALARM DRAWINGS TO BE SUBMITTED BY AWARDED CONTRACTOR

CONTACT LIST

CONTRACTOR: (24 HR. CONTACT)

JASON SMITH
STEELCO BUILDINGS, INC.
P.O. BOX 1447
COVINGTON, GEORGIA 30015

OWNER:

MIKE FRANKLIN
SOLID ROCK CHURCH
1317 NORTH CHEROKEE ROAD
SOCIAL CIRCLE, GEORGIA 30025

STRUCTURAL:

HAL MOSS
CH MOSS & ASSOCIATES, INC.
P.O. BOX 28
COVINGTON, GEORGIA 30015
GEORGIA P.E. LICENSE NO. PE00873

ELECTRICAL:

TIM LEE
TL ENGINEERING, LLC
5842 NORFOLK CHASE ROAD
PEACHTREE CORNERS, GEORGIA 30092
GEORGIA P.E. LICENSE NO. PE037597

TEL#: 678-439-8664

MECHANICAL:

WILLIAM E. DUNN
PREFERRED ENGINEERING SOLUTIONS, INC.
597 UNIT NO.7 HIAWASSEE ESTATES DRIVE
HIAWASSEE, GEORGIA 30546
GEORGIA P.E. LICENSE NO. PE06825

TEL#: 770-601-0636

CIVIL:

NICK ROPER
BEAR CREEK ENGINEERING
10384 FIELDCREST DRIVE, SUITE C
COVINGTON, GEORGIA 30014
GEORGIA P.E. LICENSE NO. PE35110



SteelCo
BUILDINGS, INC.

PO Box 1447 • Covington, GA 30015
ph 678-212-2190
www.steelcobuildings.com

[illegible]

SHEET TITLE


COVER SHEET


PROJECT NAME & LOCATION

SOLID ROCK BAPTIST CHURCH
NEW FACILITY


U.S. HIGHWAY 278
SOCIAL CIRCLE, GA 30025





SCALE		AS SHOWN	
PROJECT NO		C21-0024	
BY	KRB	CS-1	
DATE	2-10-2022		
		SHEET	

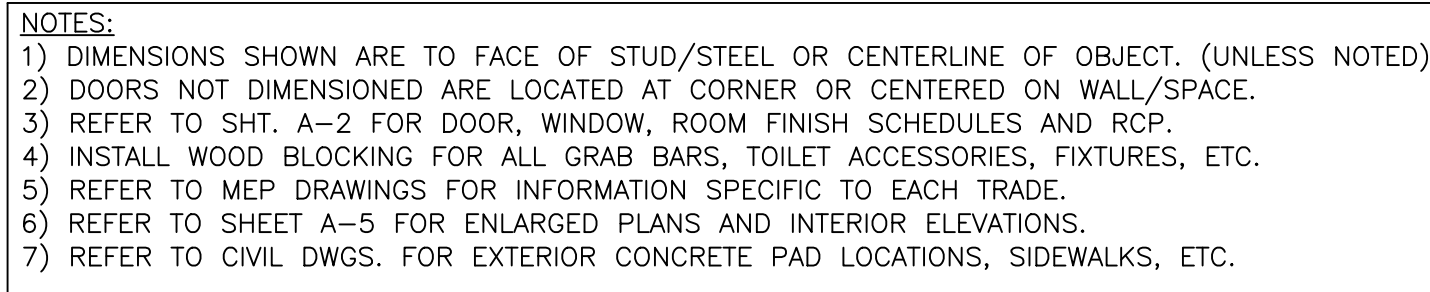

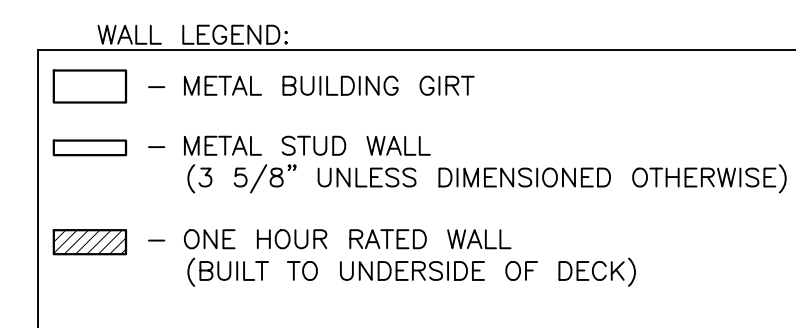









SCALE		AS SHOWN	
PROJECT NO C21-0024			
BY KRB		A-1.1	
DATE 2-10-2022			
		SHEET	

 

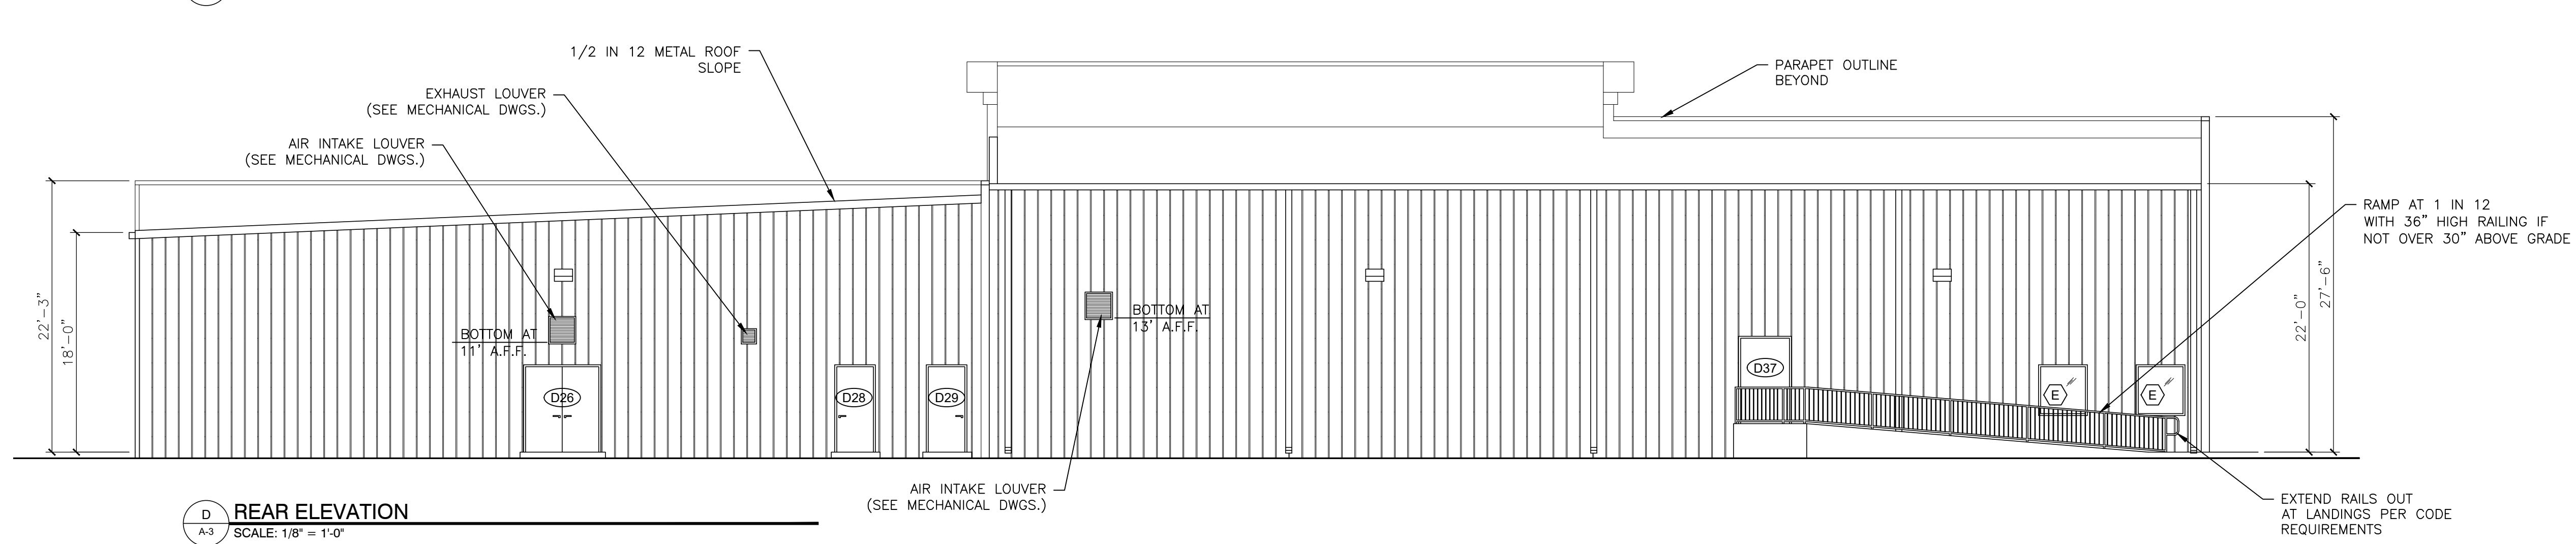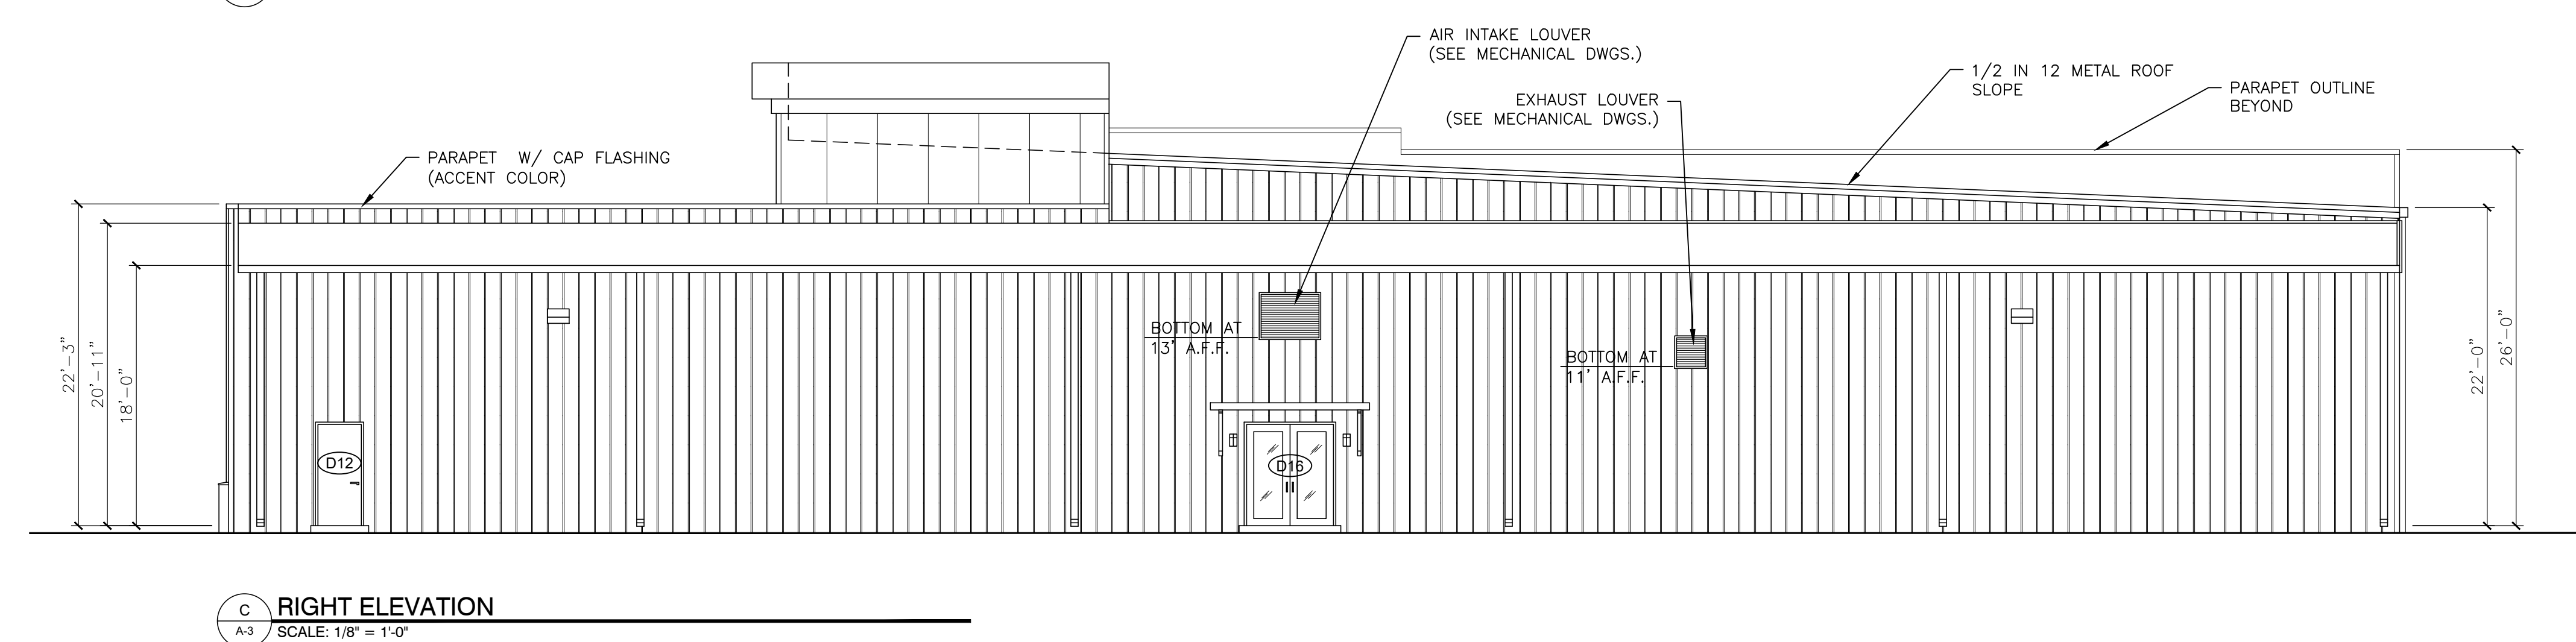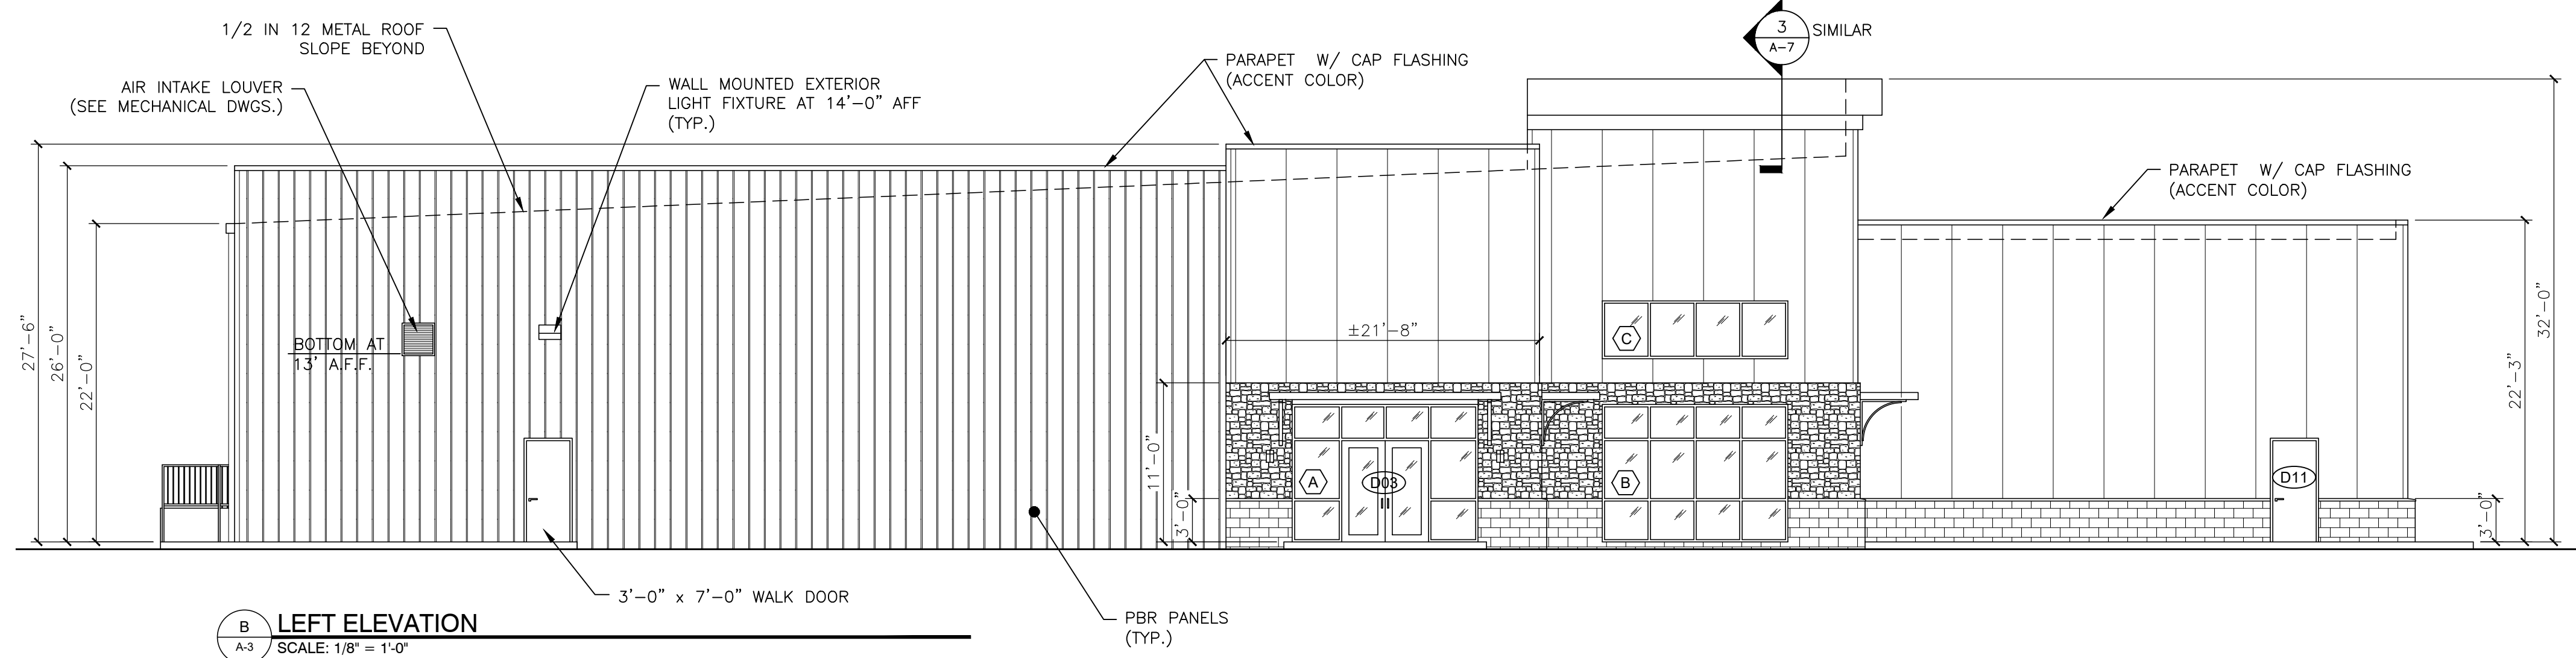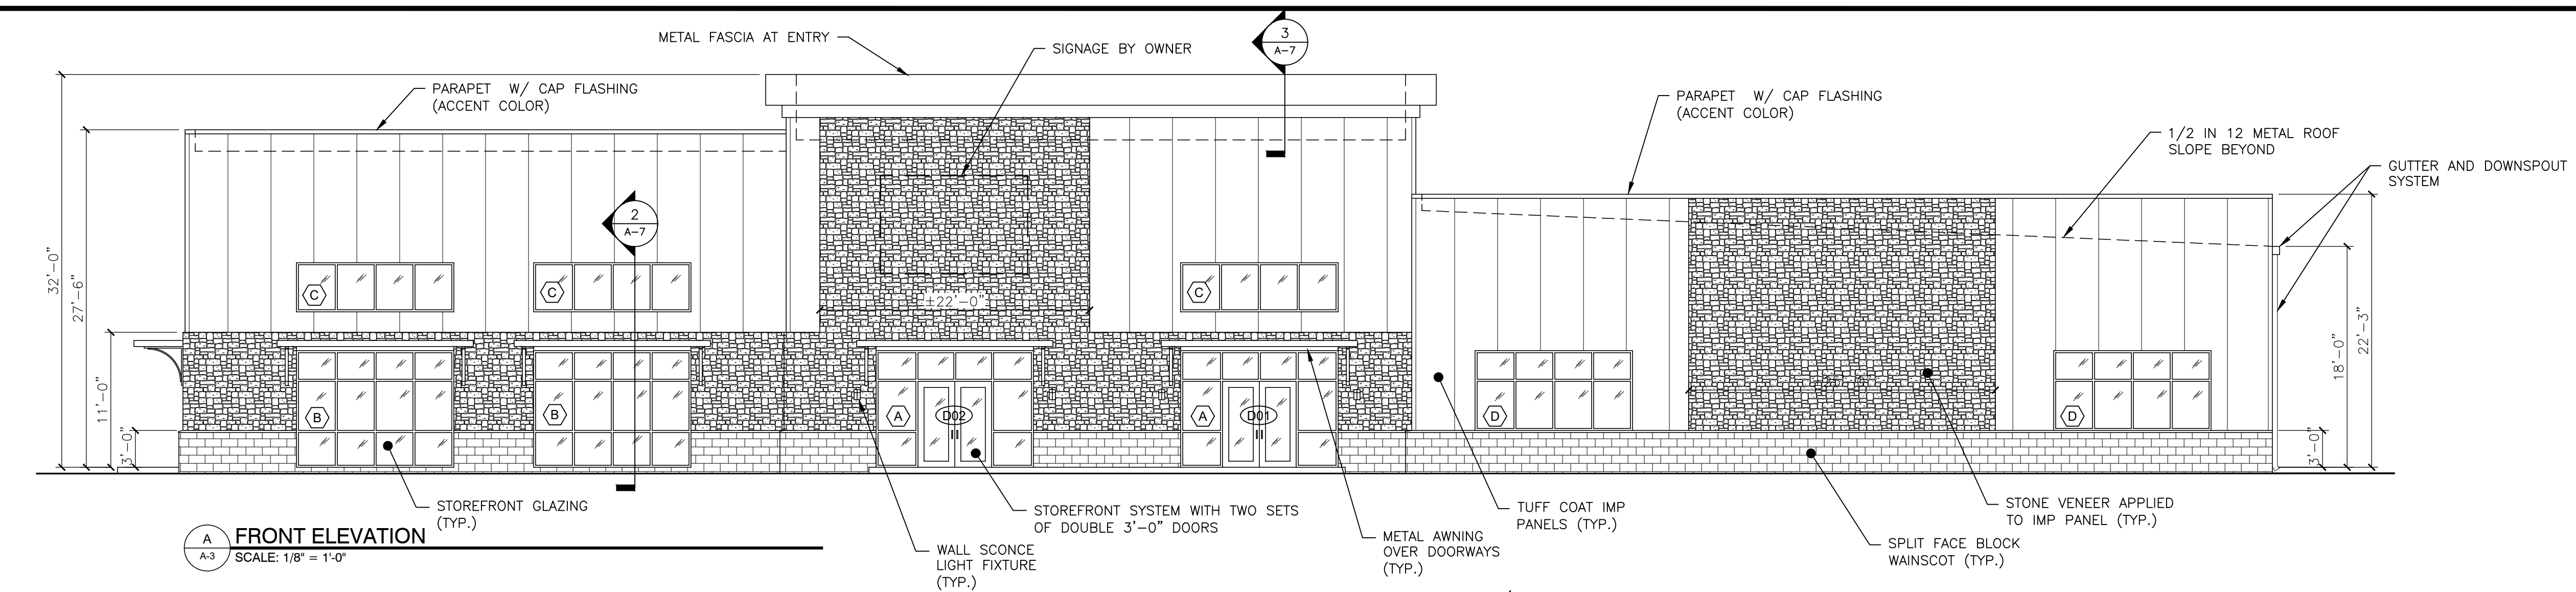[illegible]

SHEET TITLE	PROJECT NAME & LOCATION
EXTERIOR ELEVATIONS	SOLID ROCK BAPTIST CHURCH NEW FACILITY U.S. HIGHWAY 278 SOCIAL CIRCLE, GA 30025

SCALE AS SHOWN	
PROJECT NO C21-0024	
BY KRB	A-3 SHEET
DATE 2-10-2022	

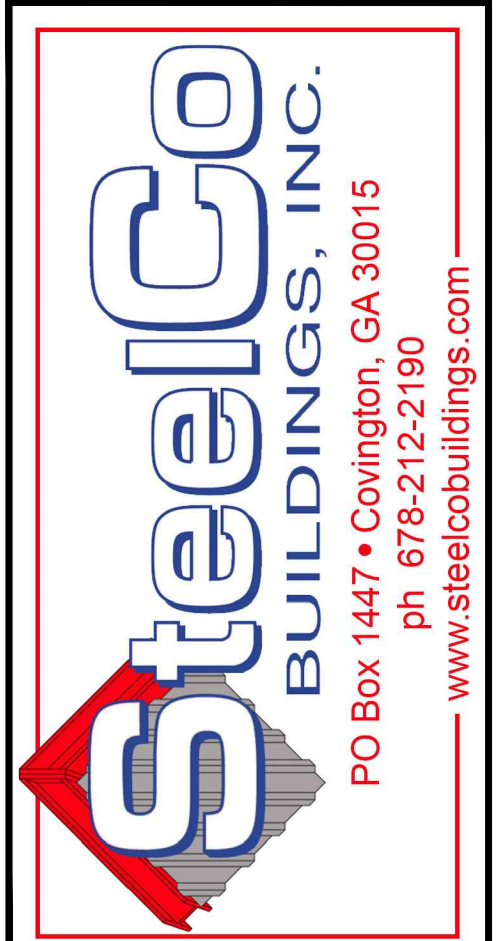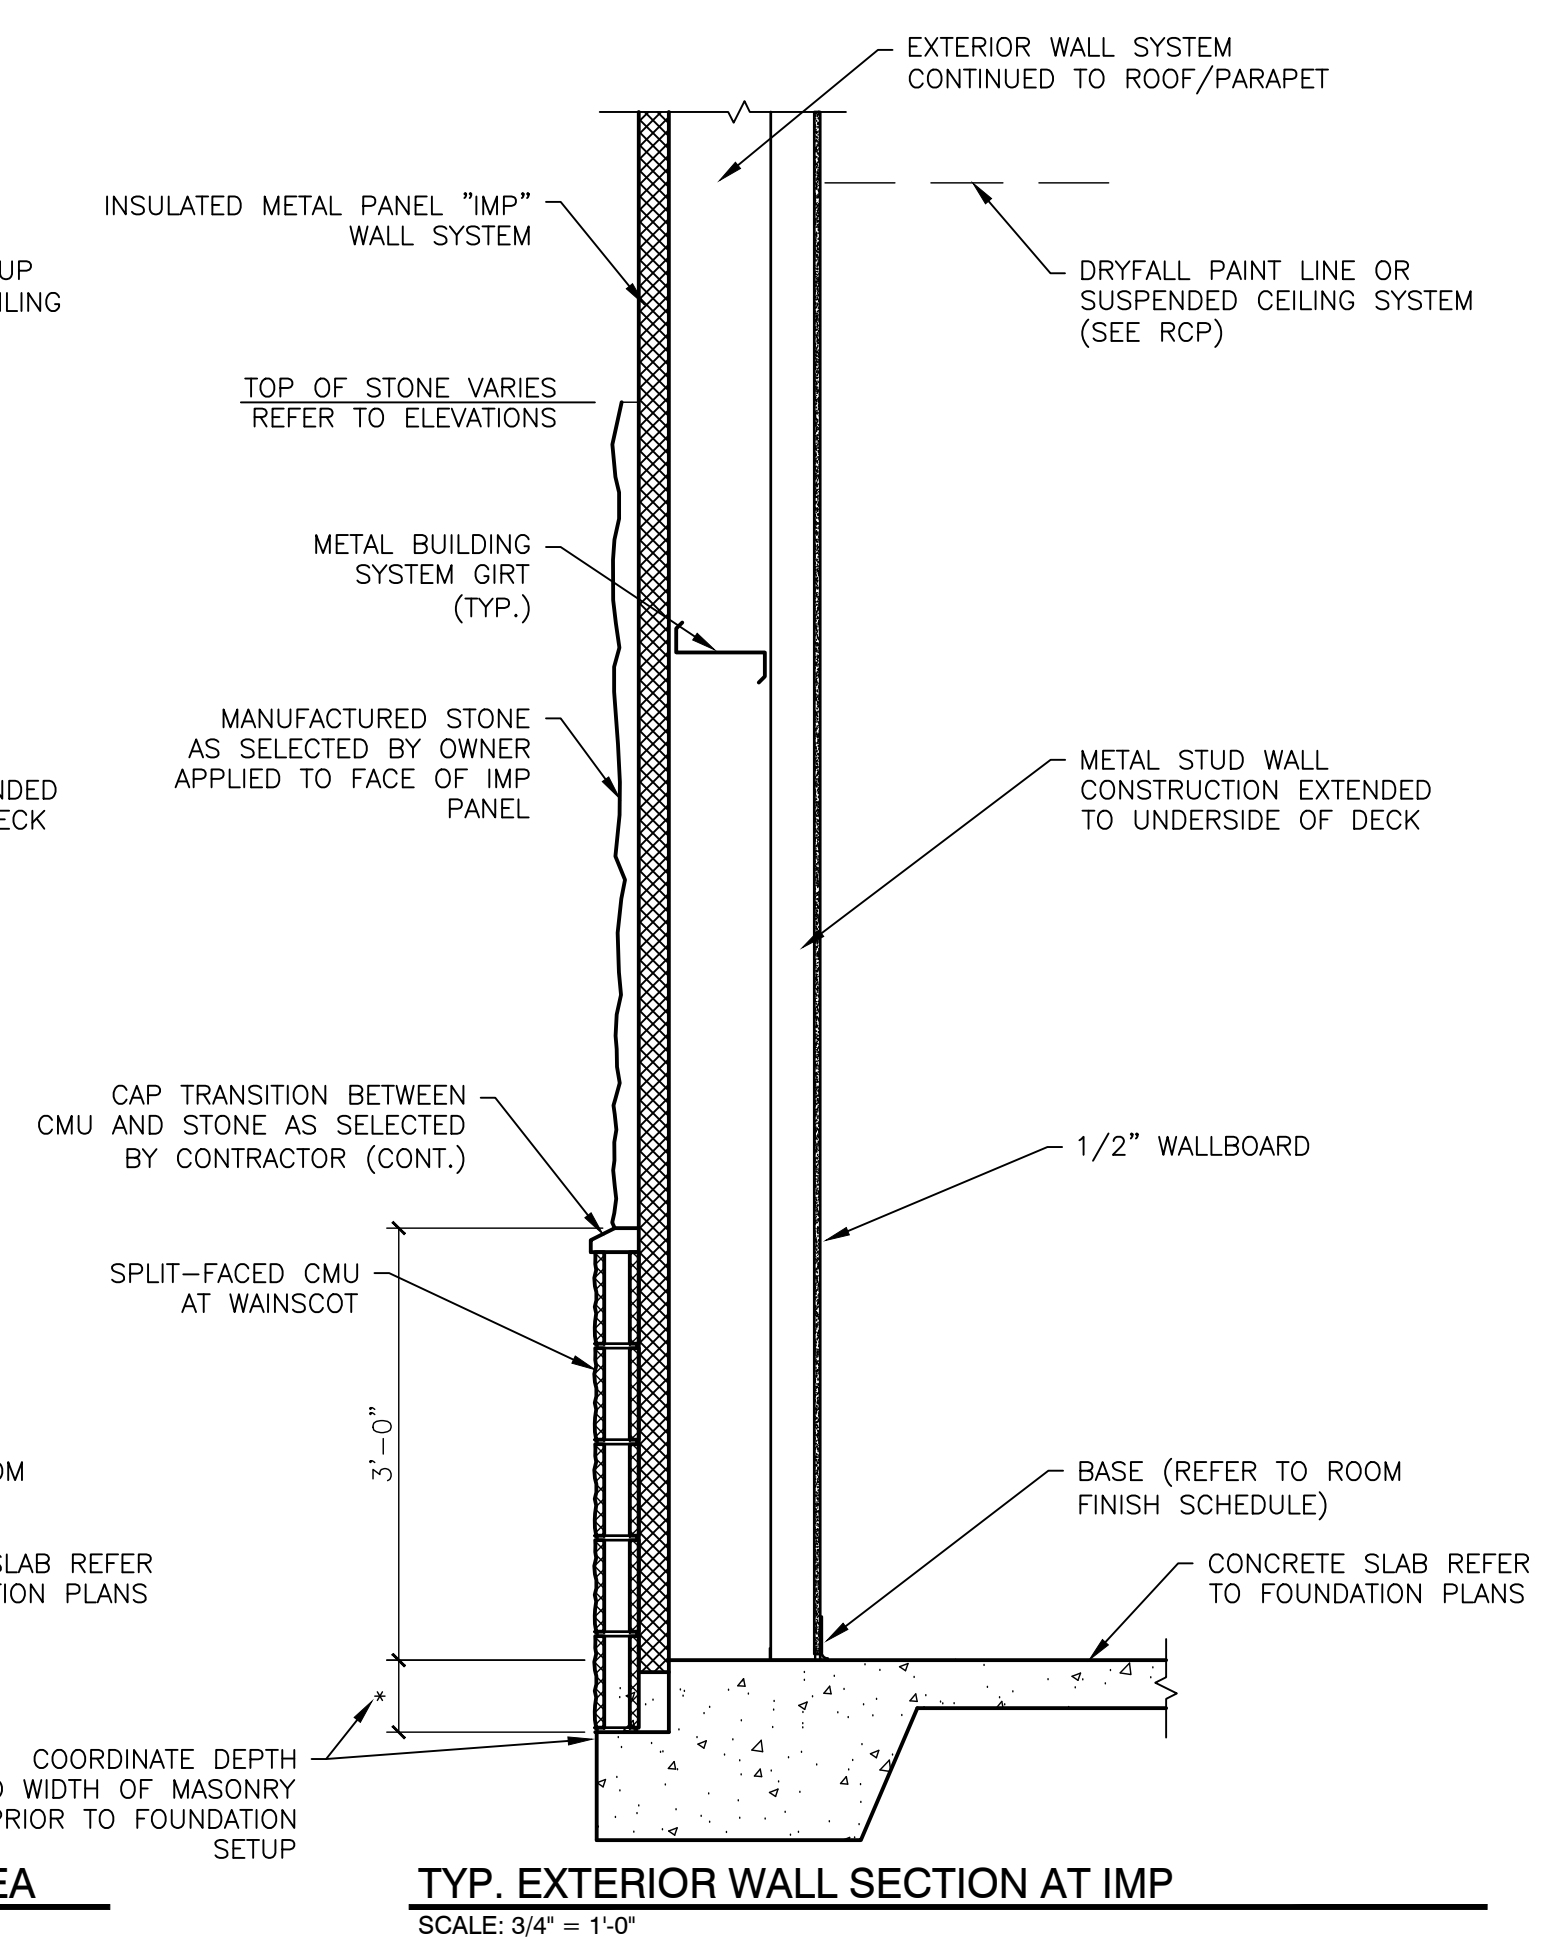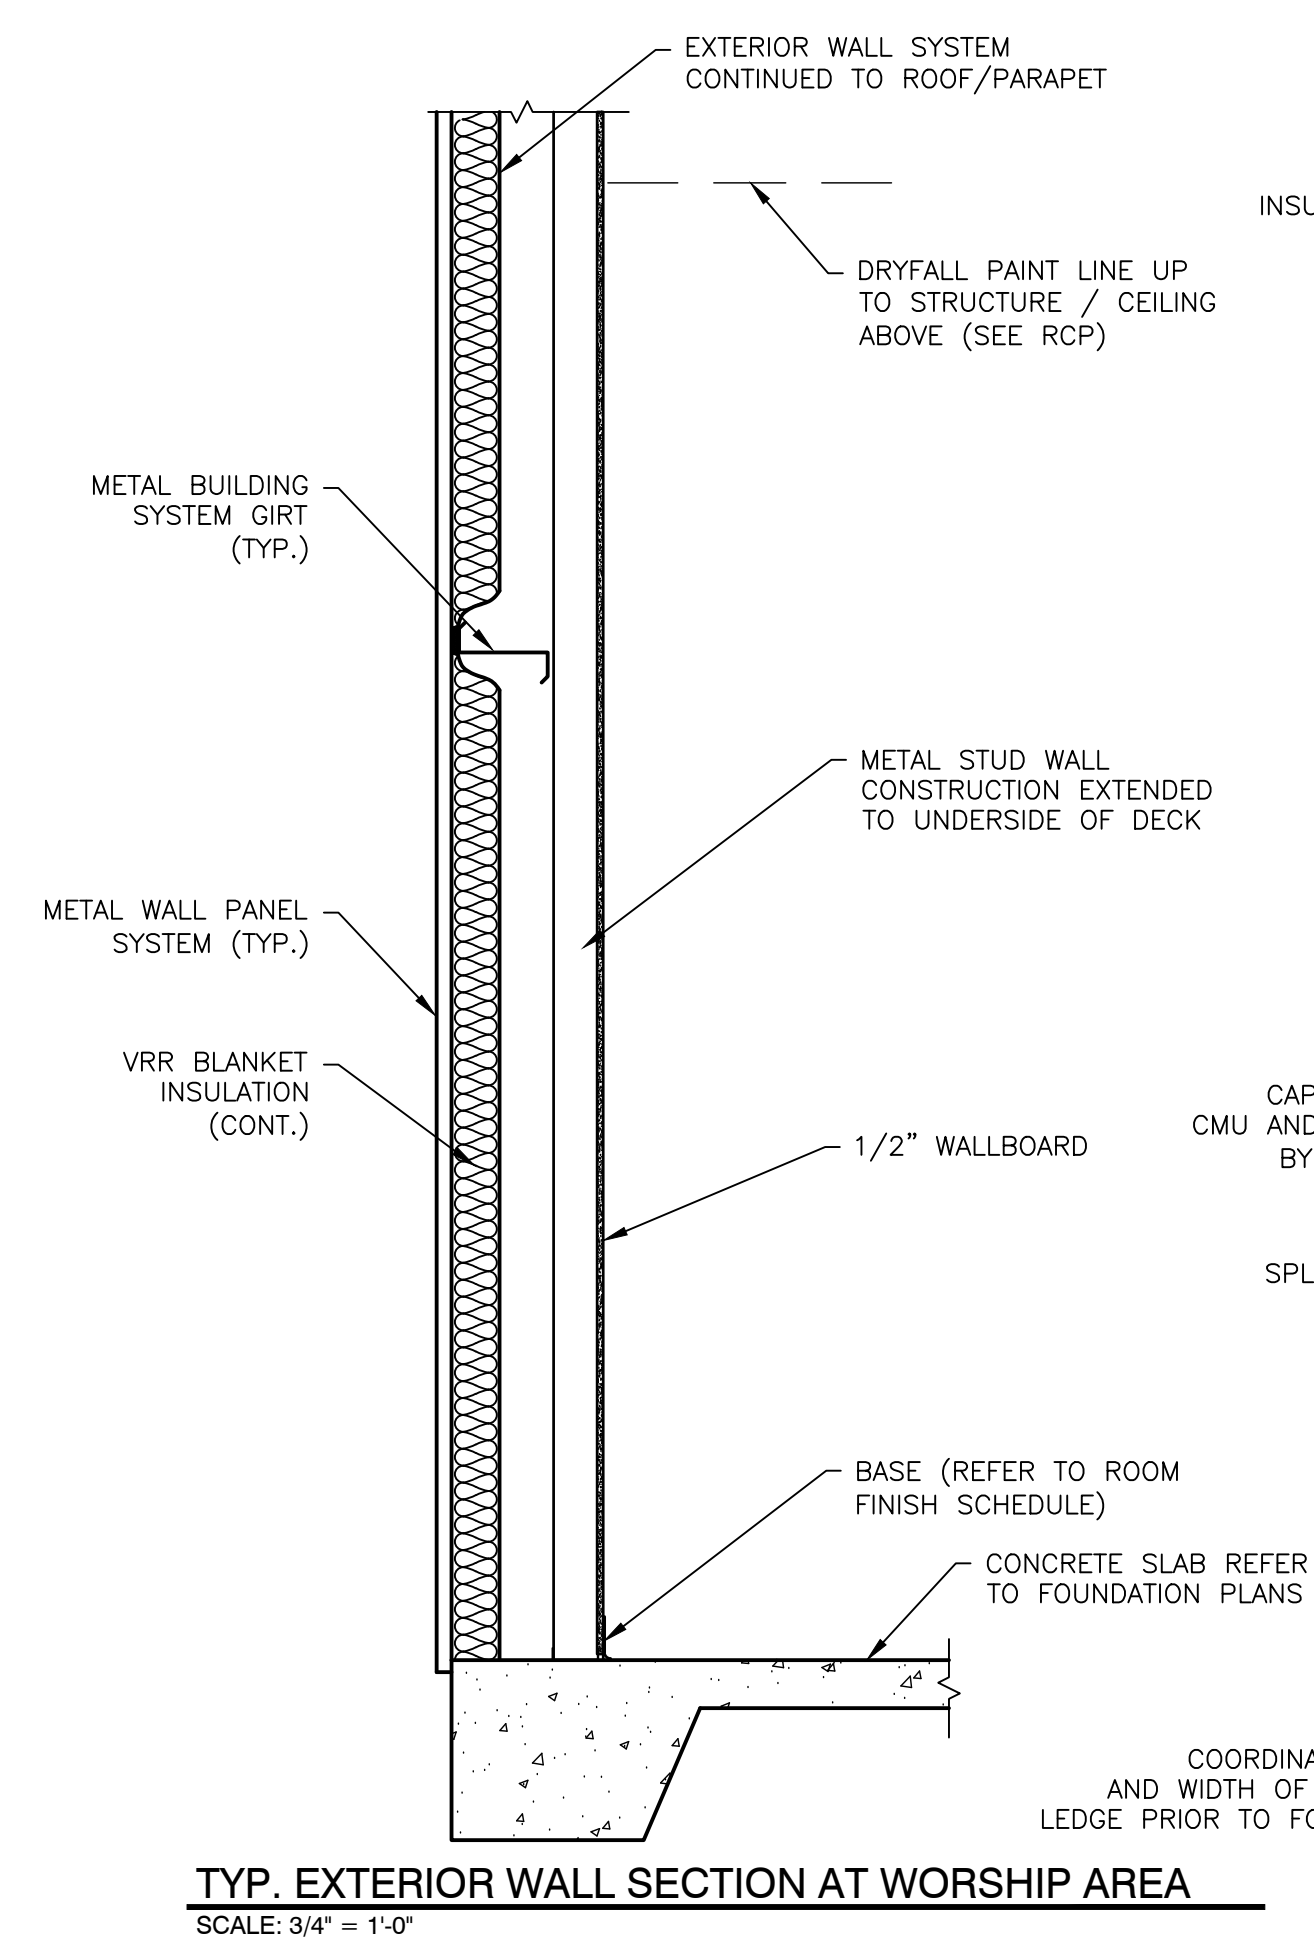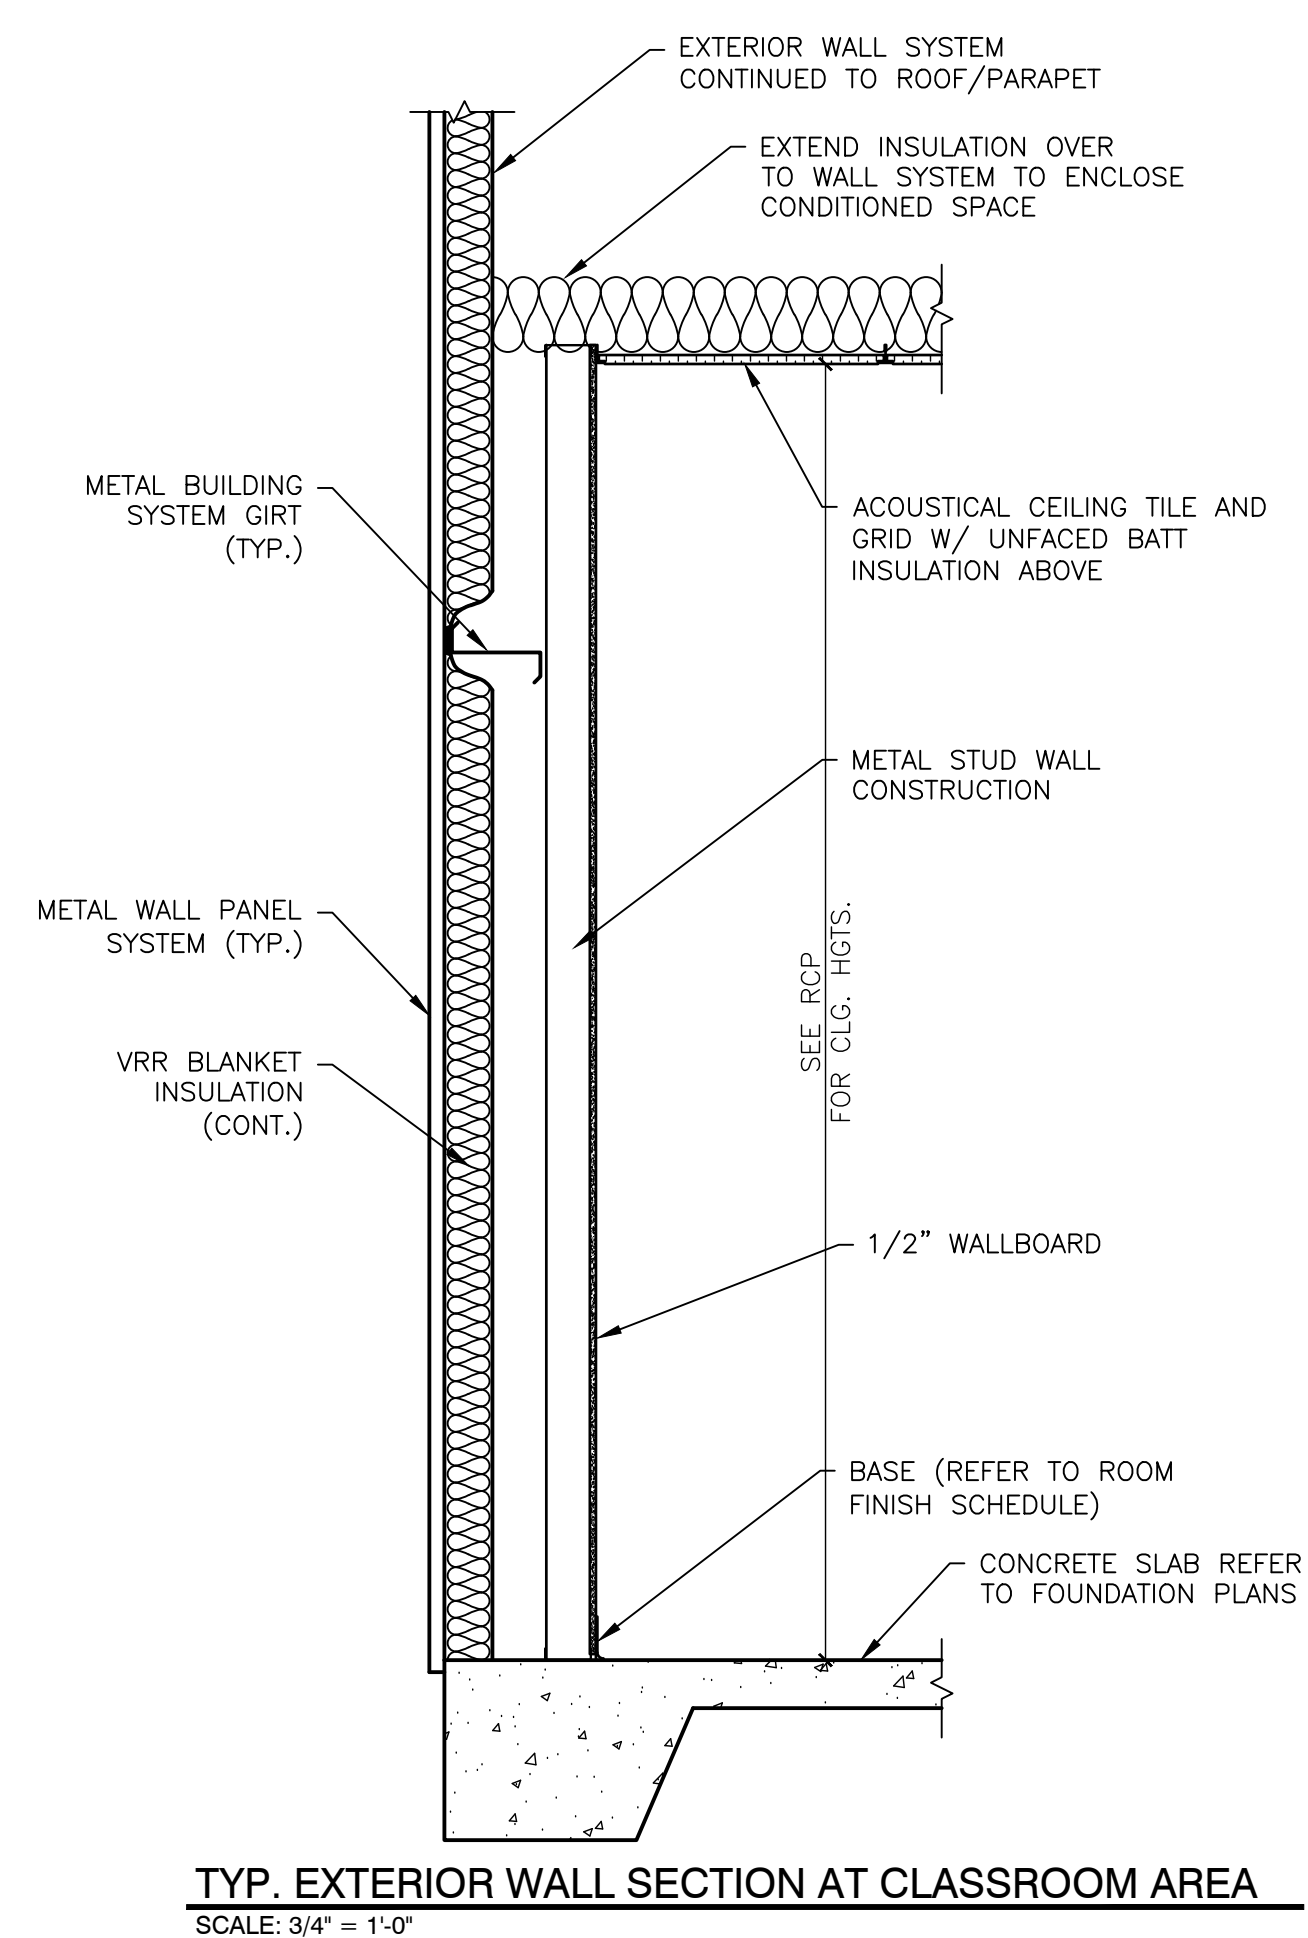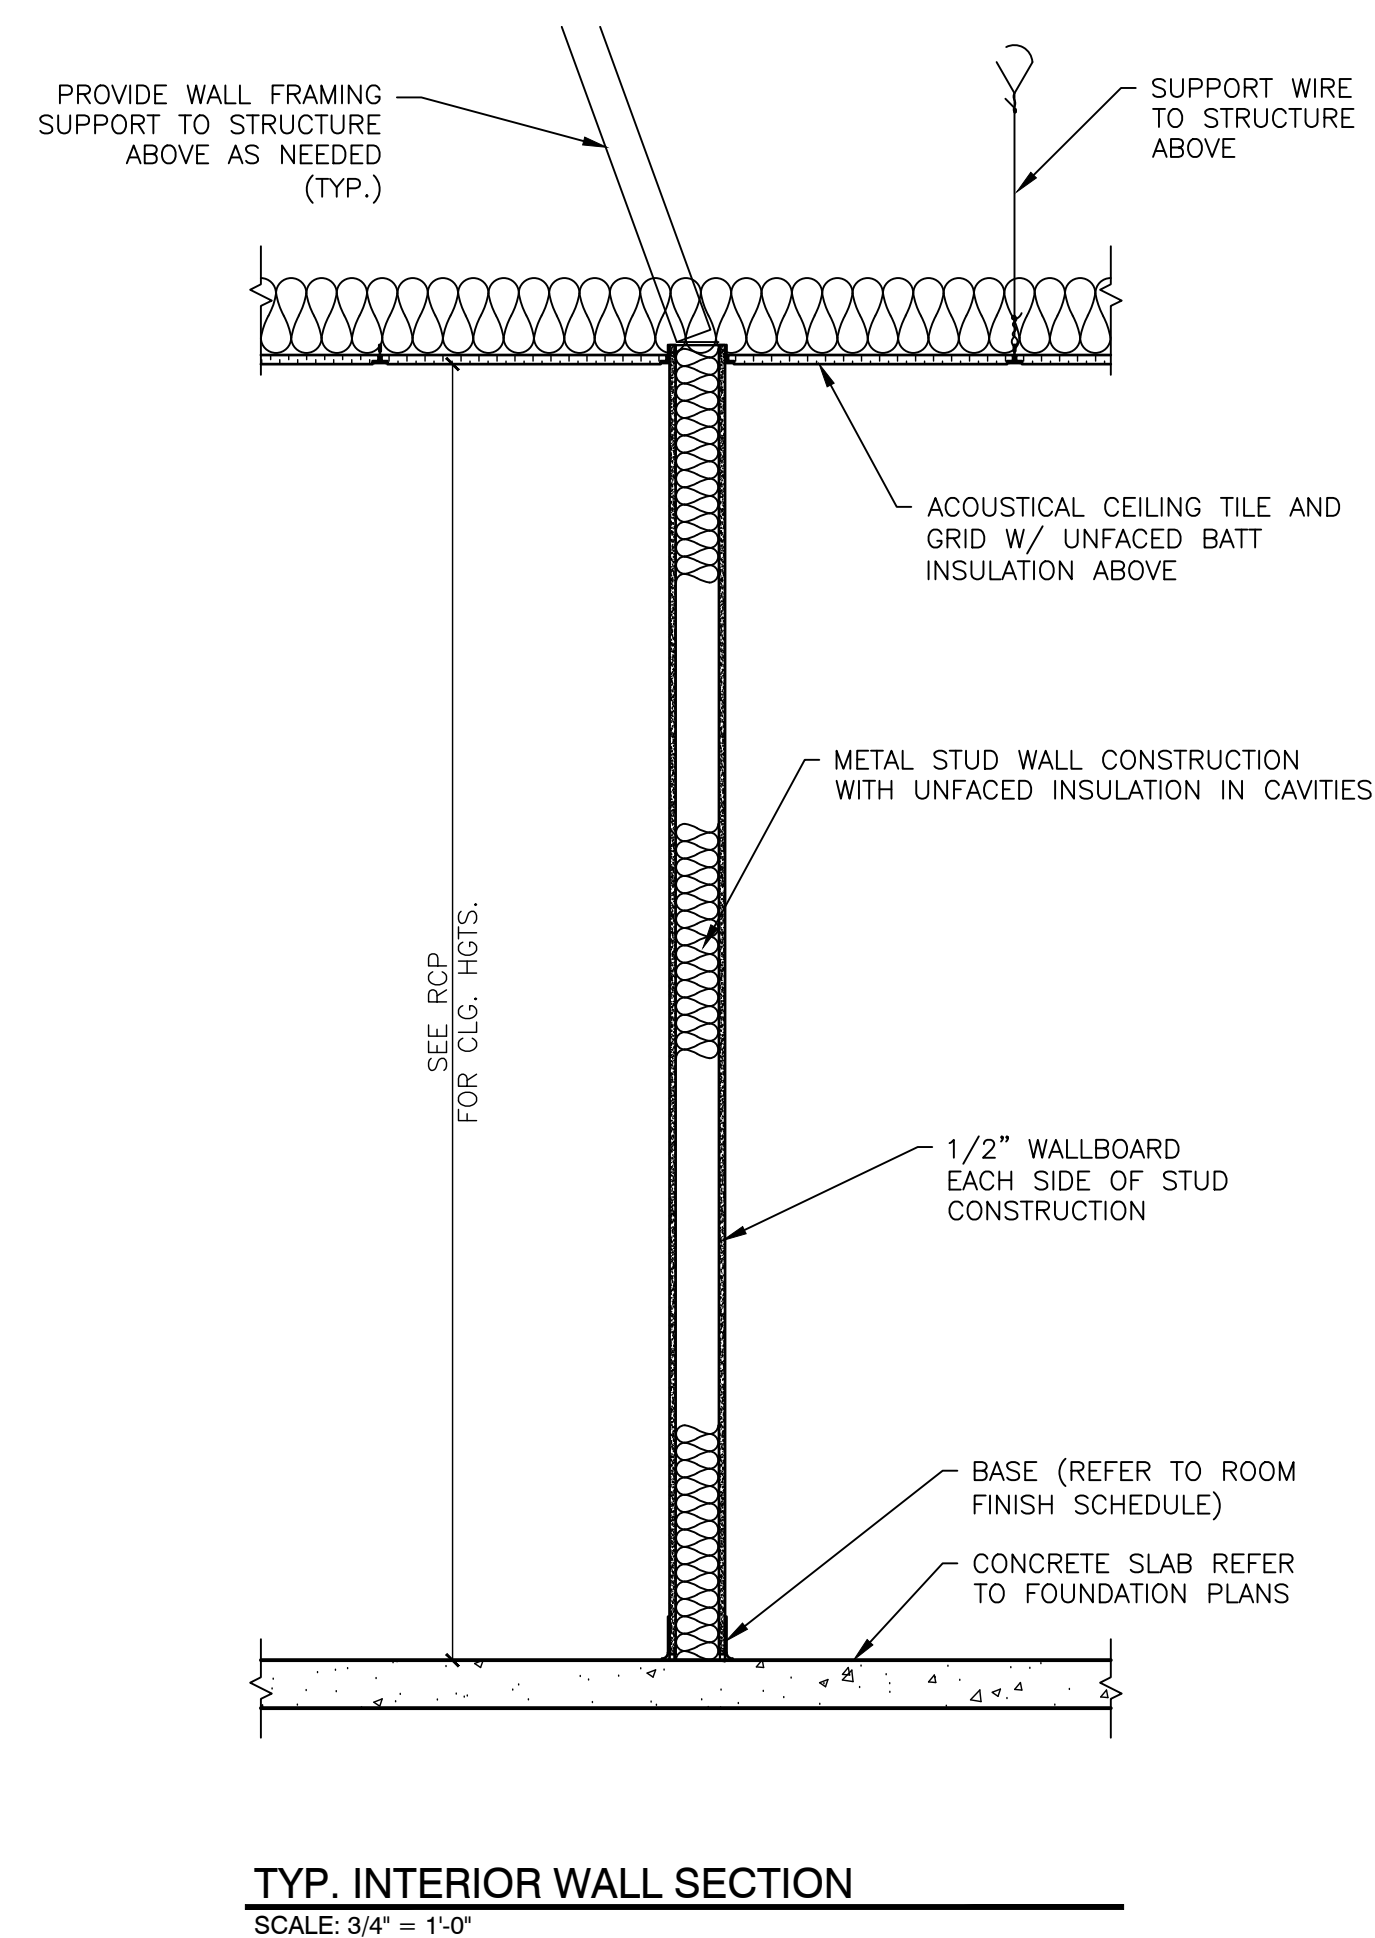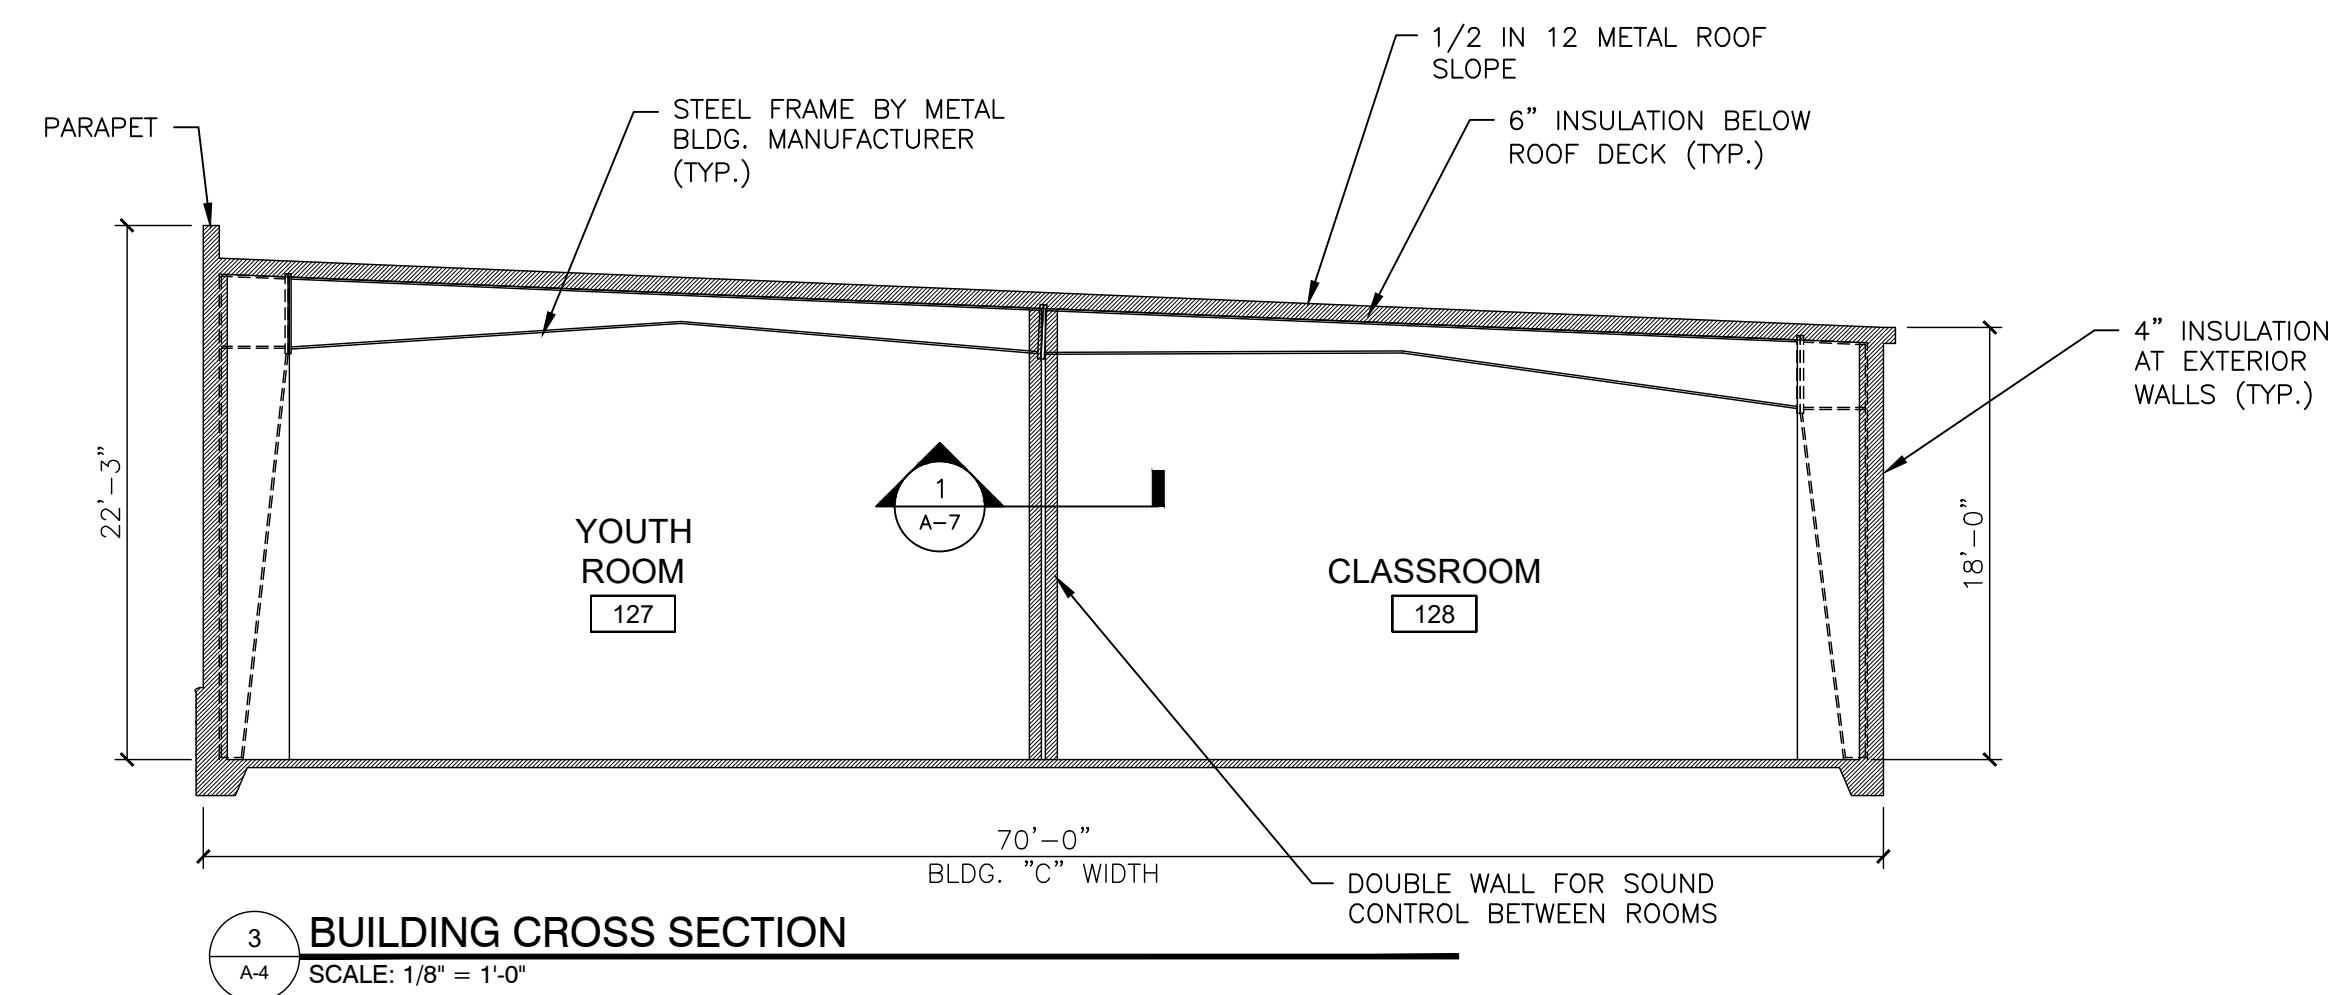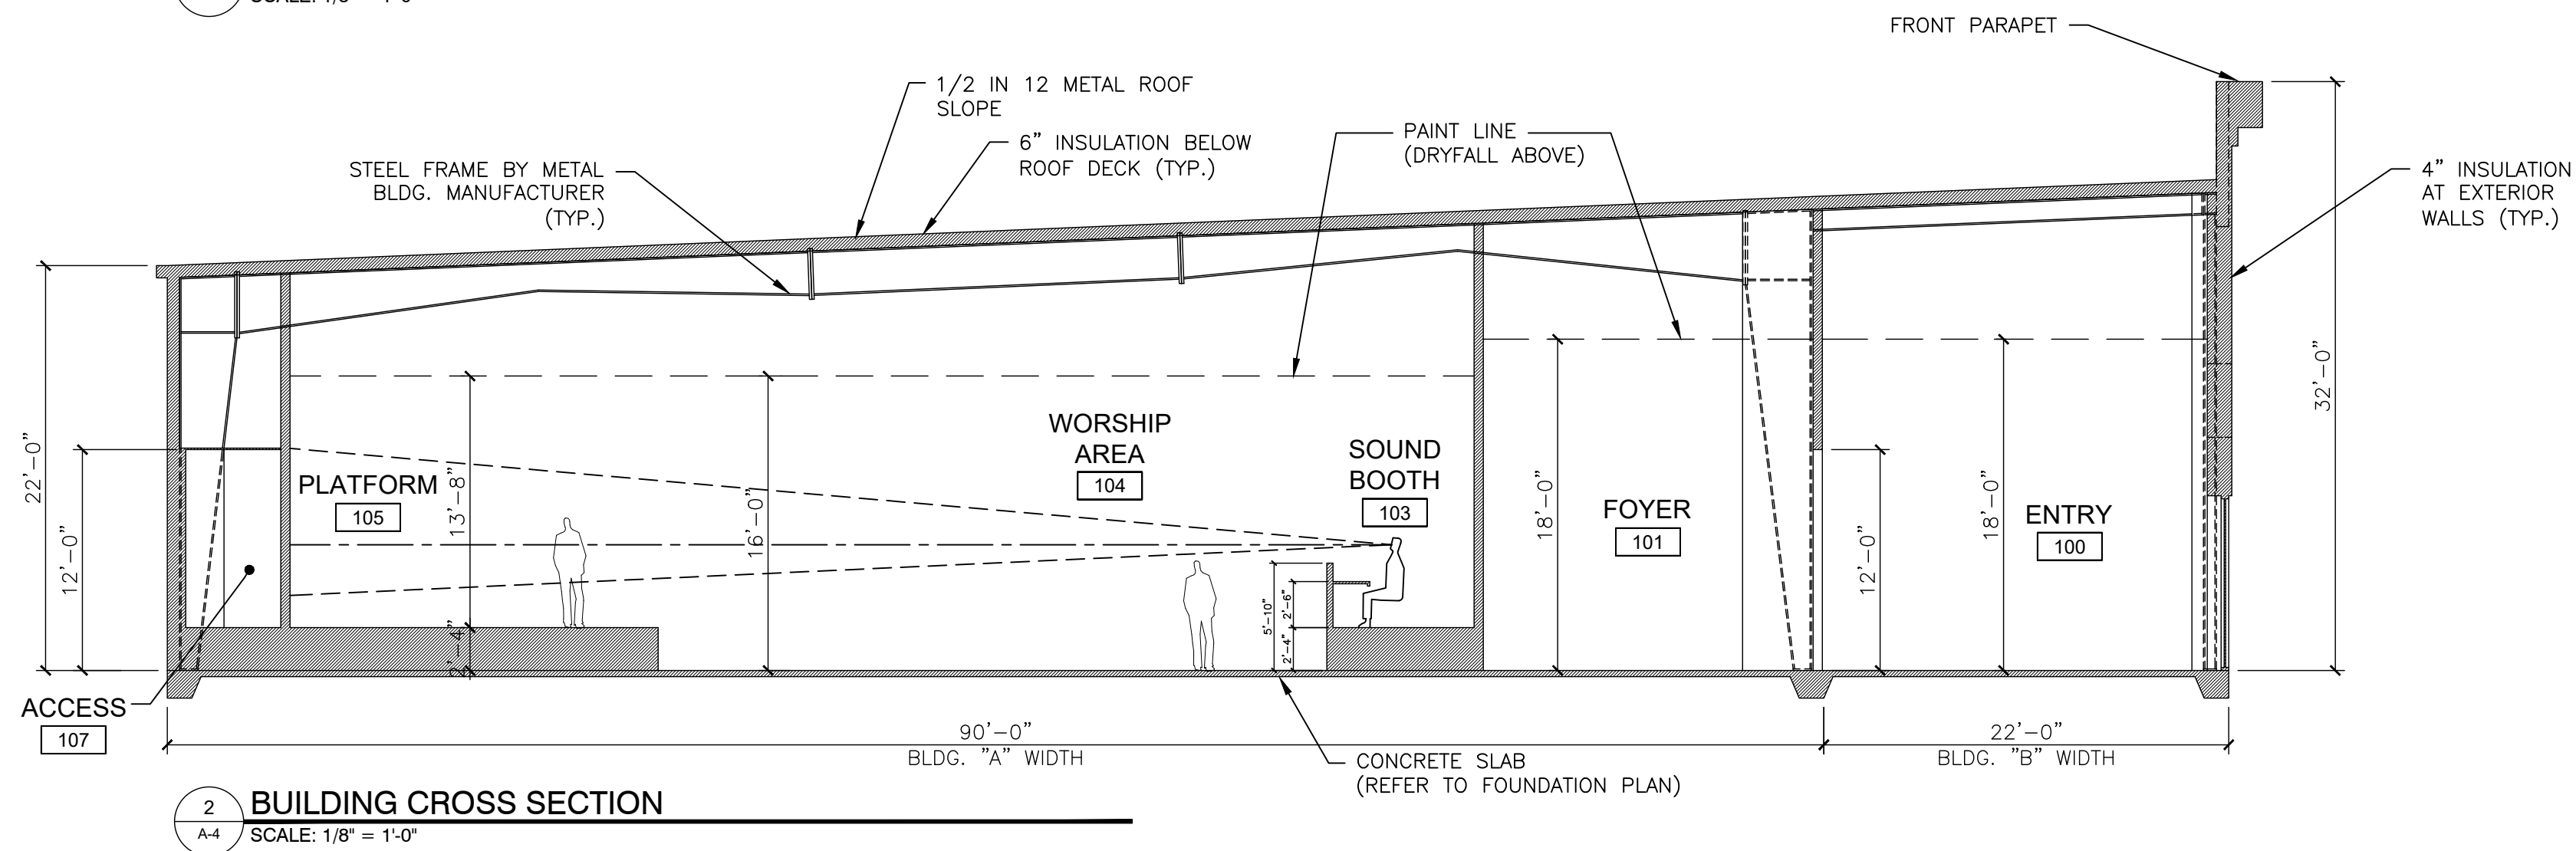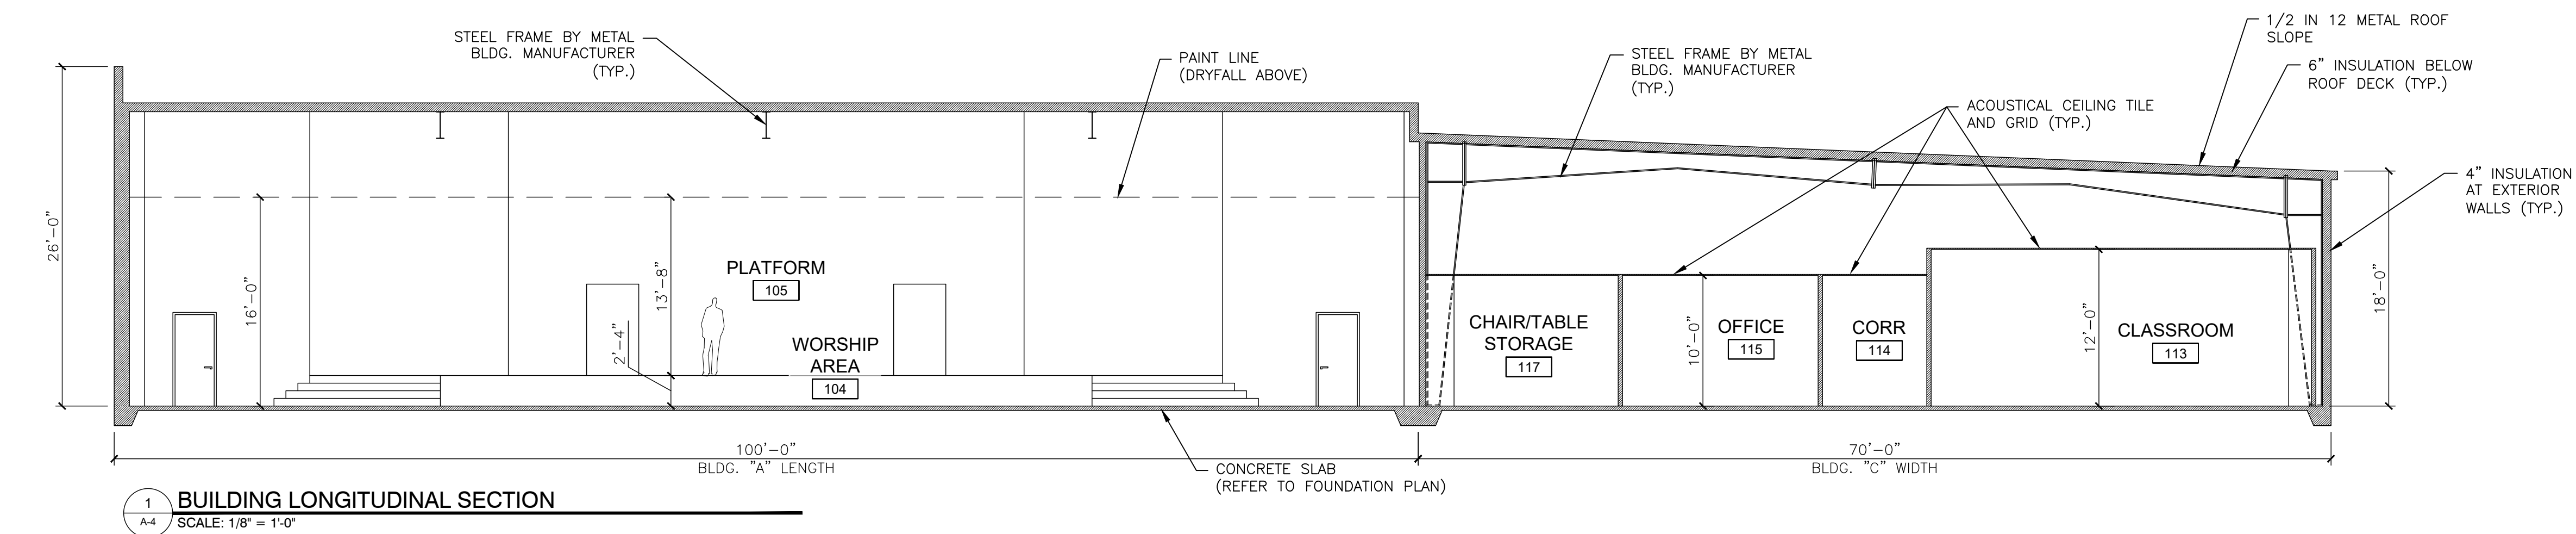[illegible]

SHEET TITLE

BLDG. & WALL SECTIONS

DATE: 11/11/2015

BY: J. L. HARRIS

PROJECT NAME & LOCATION
**SOLID ROCK BAPTIST CHURCH
NEW FACILITY**
U.S. HIGHWAY 278
SOCIAL CIRCLE, GA 30025


SCALE AS SHOWN








PROJECT NO
C21-0024

BY KRB

DATE	2-10-2022
------	-----------

 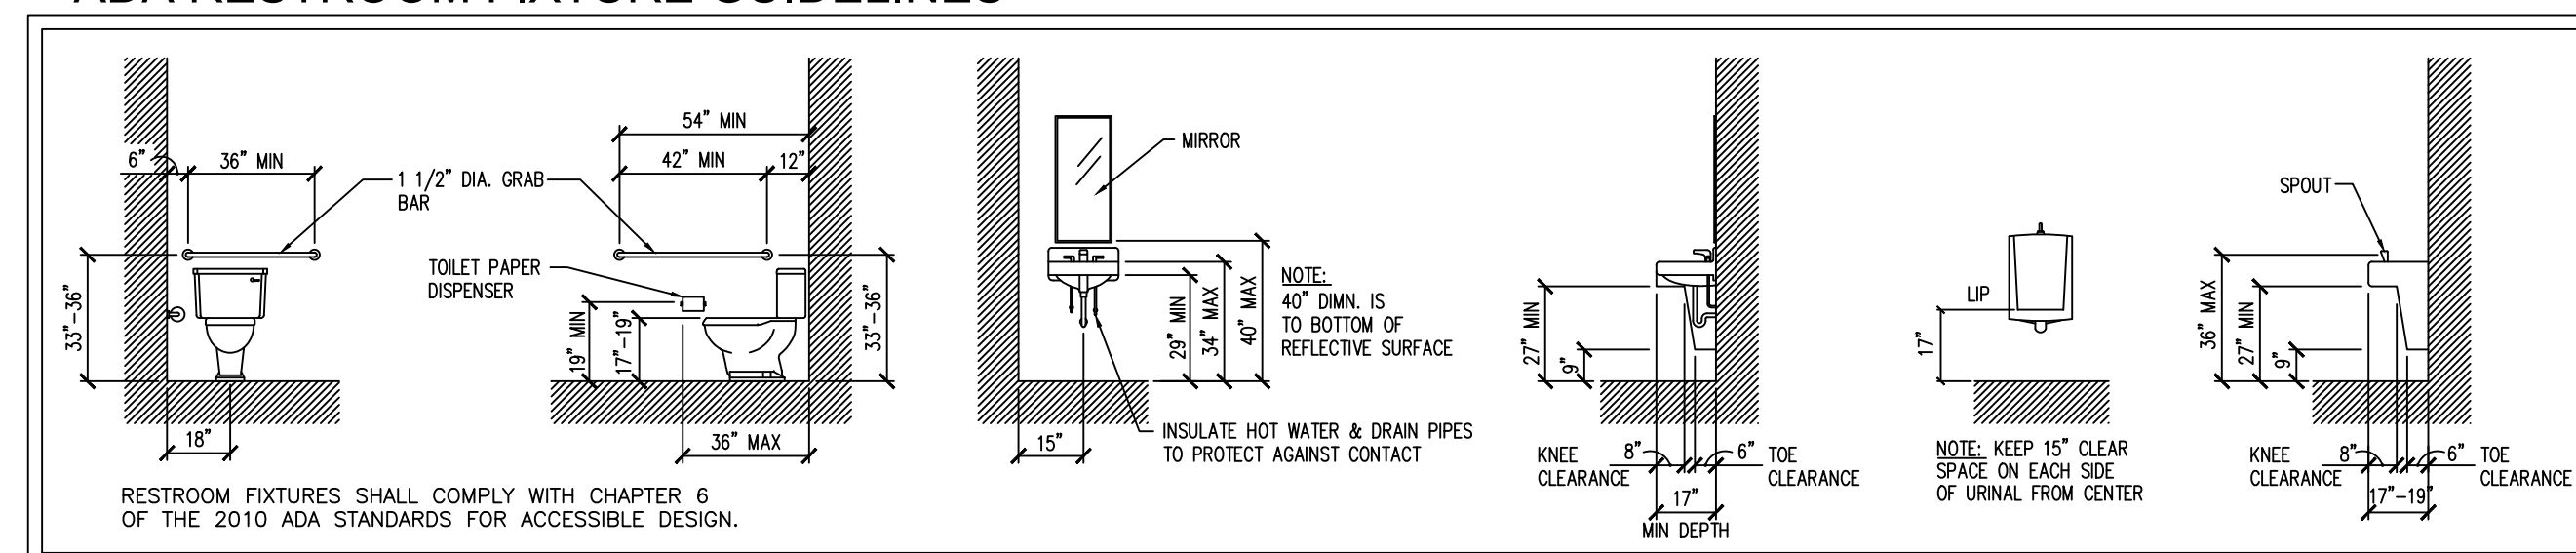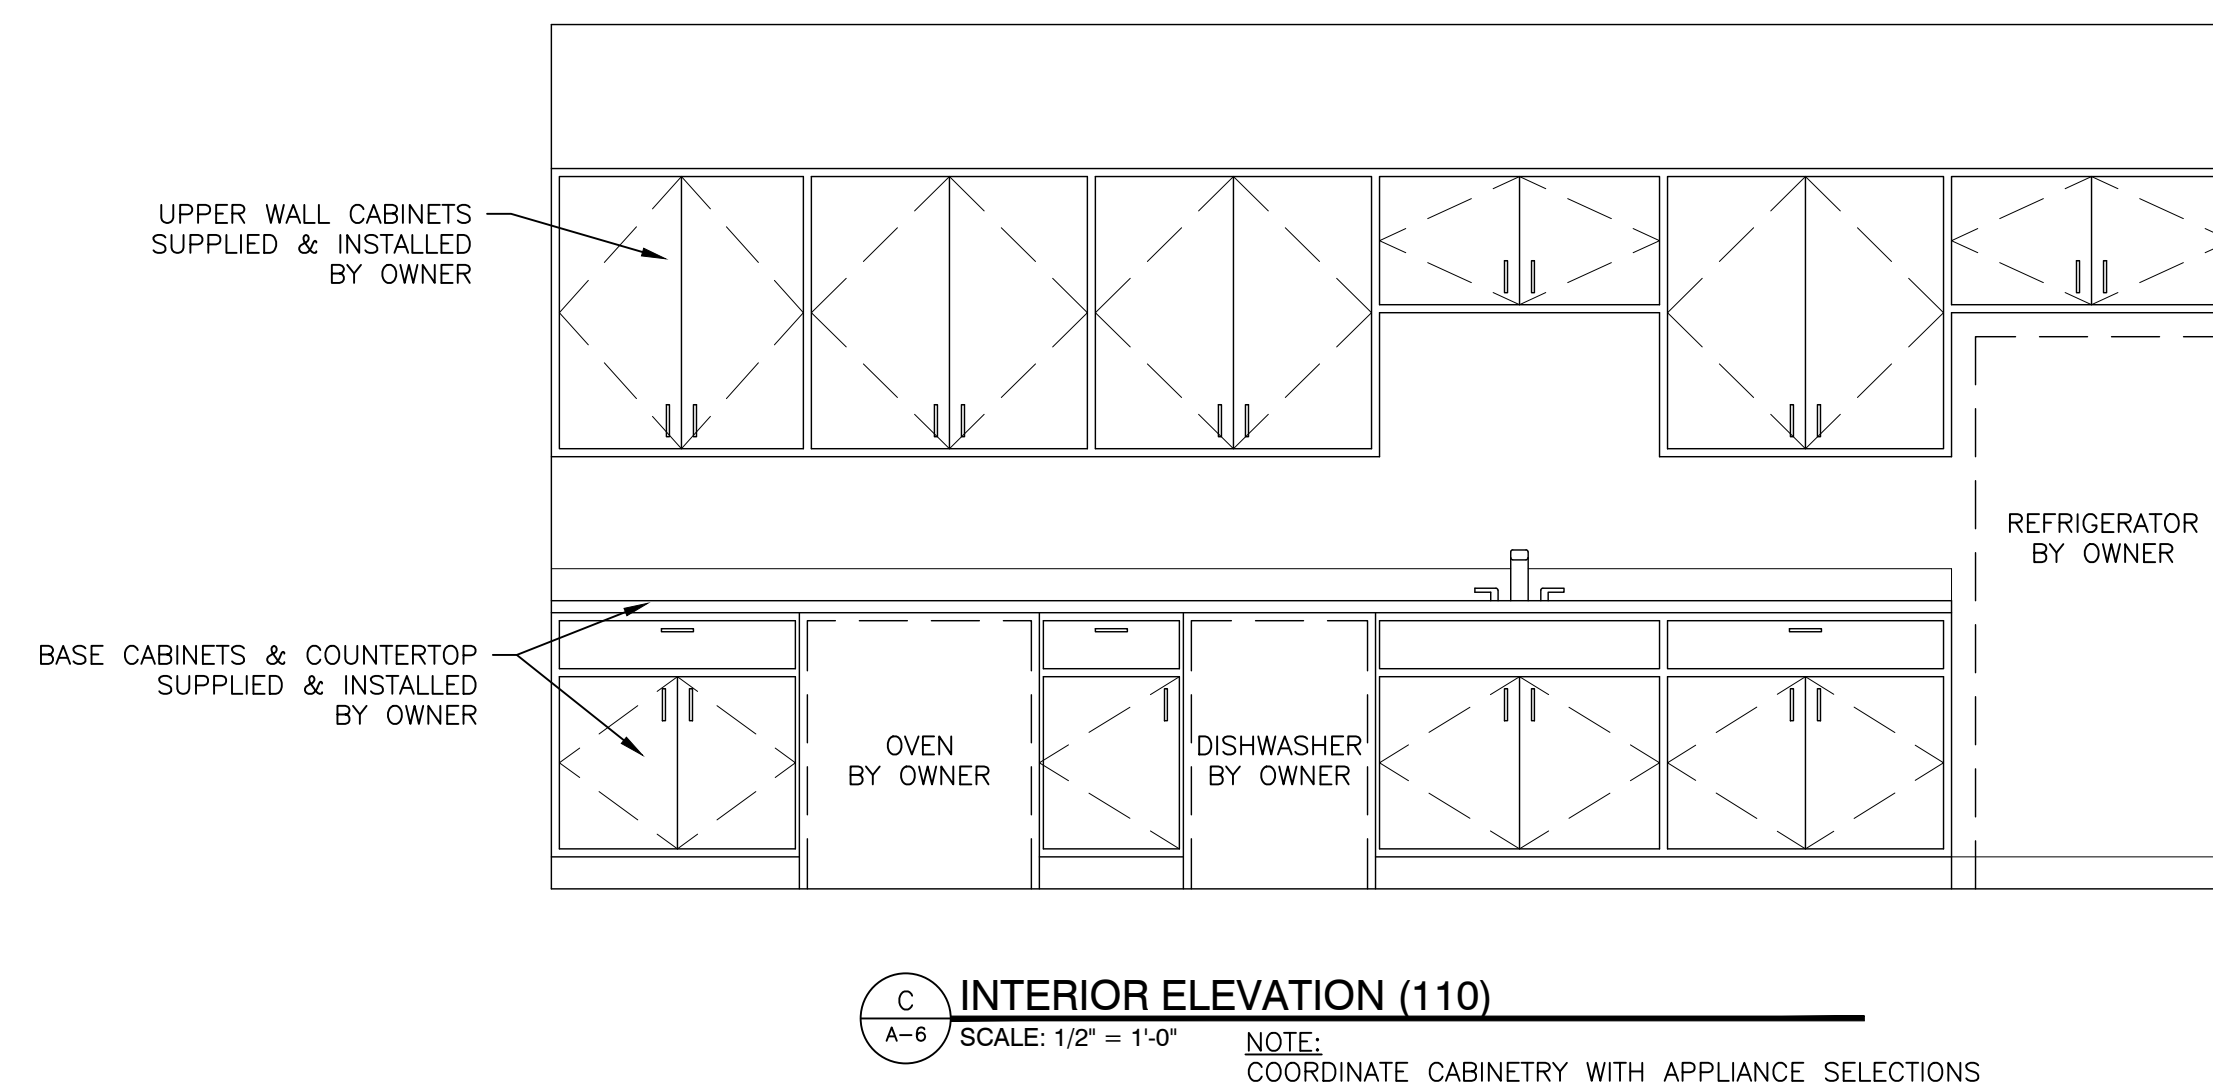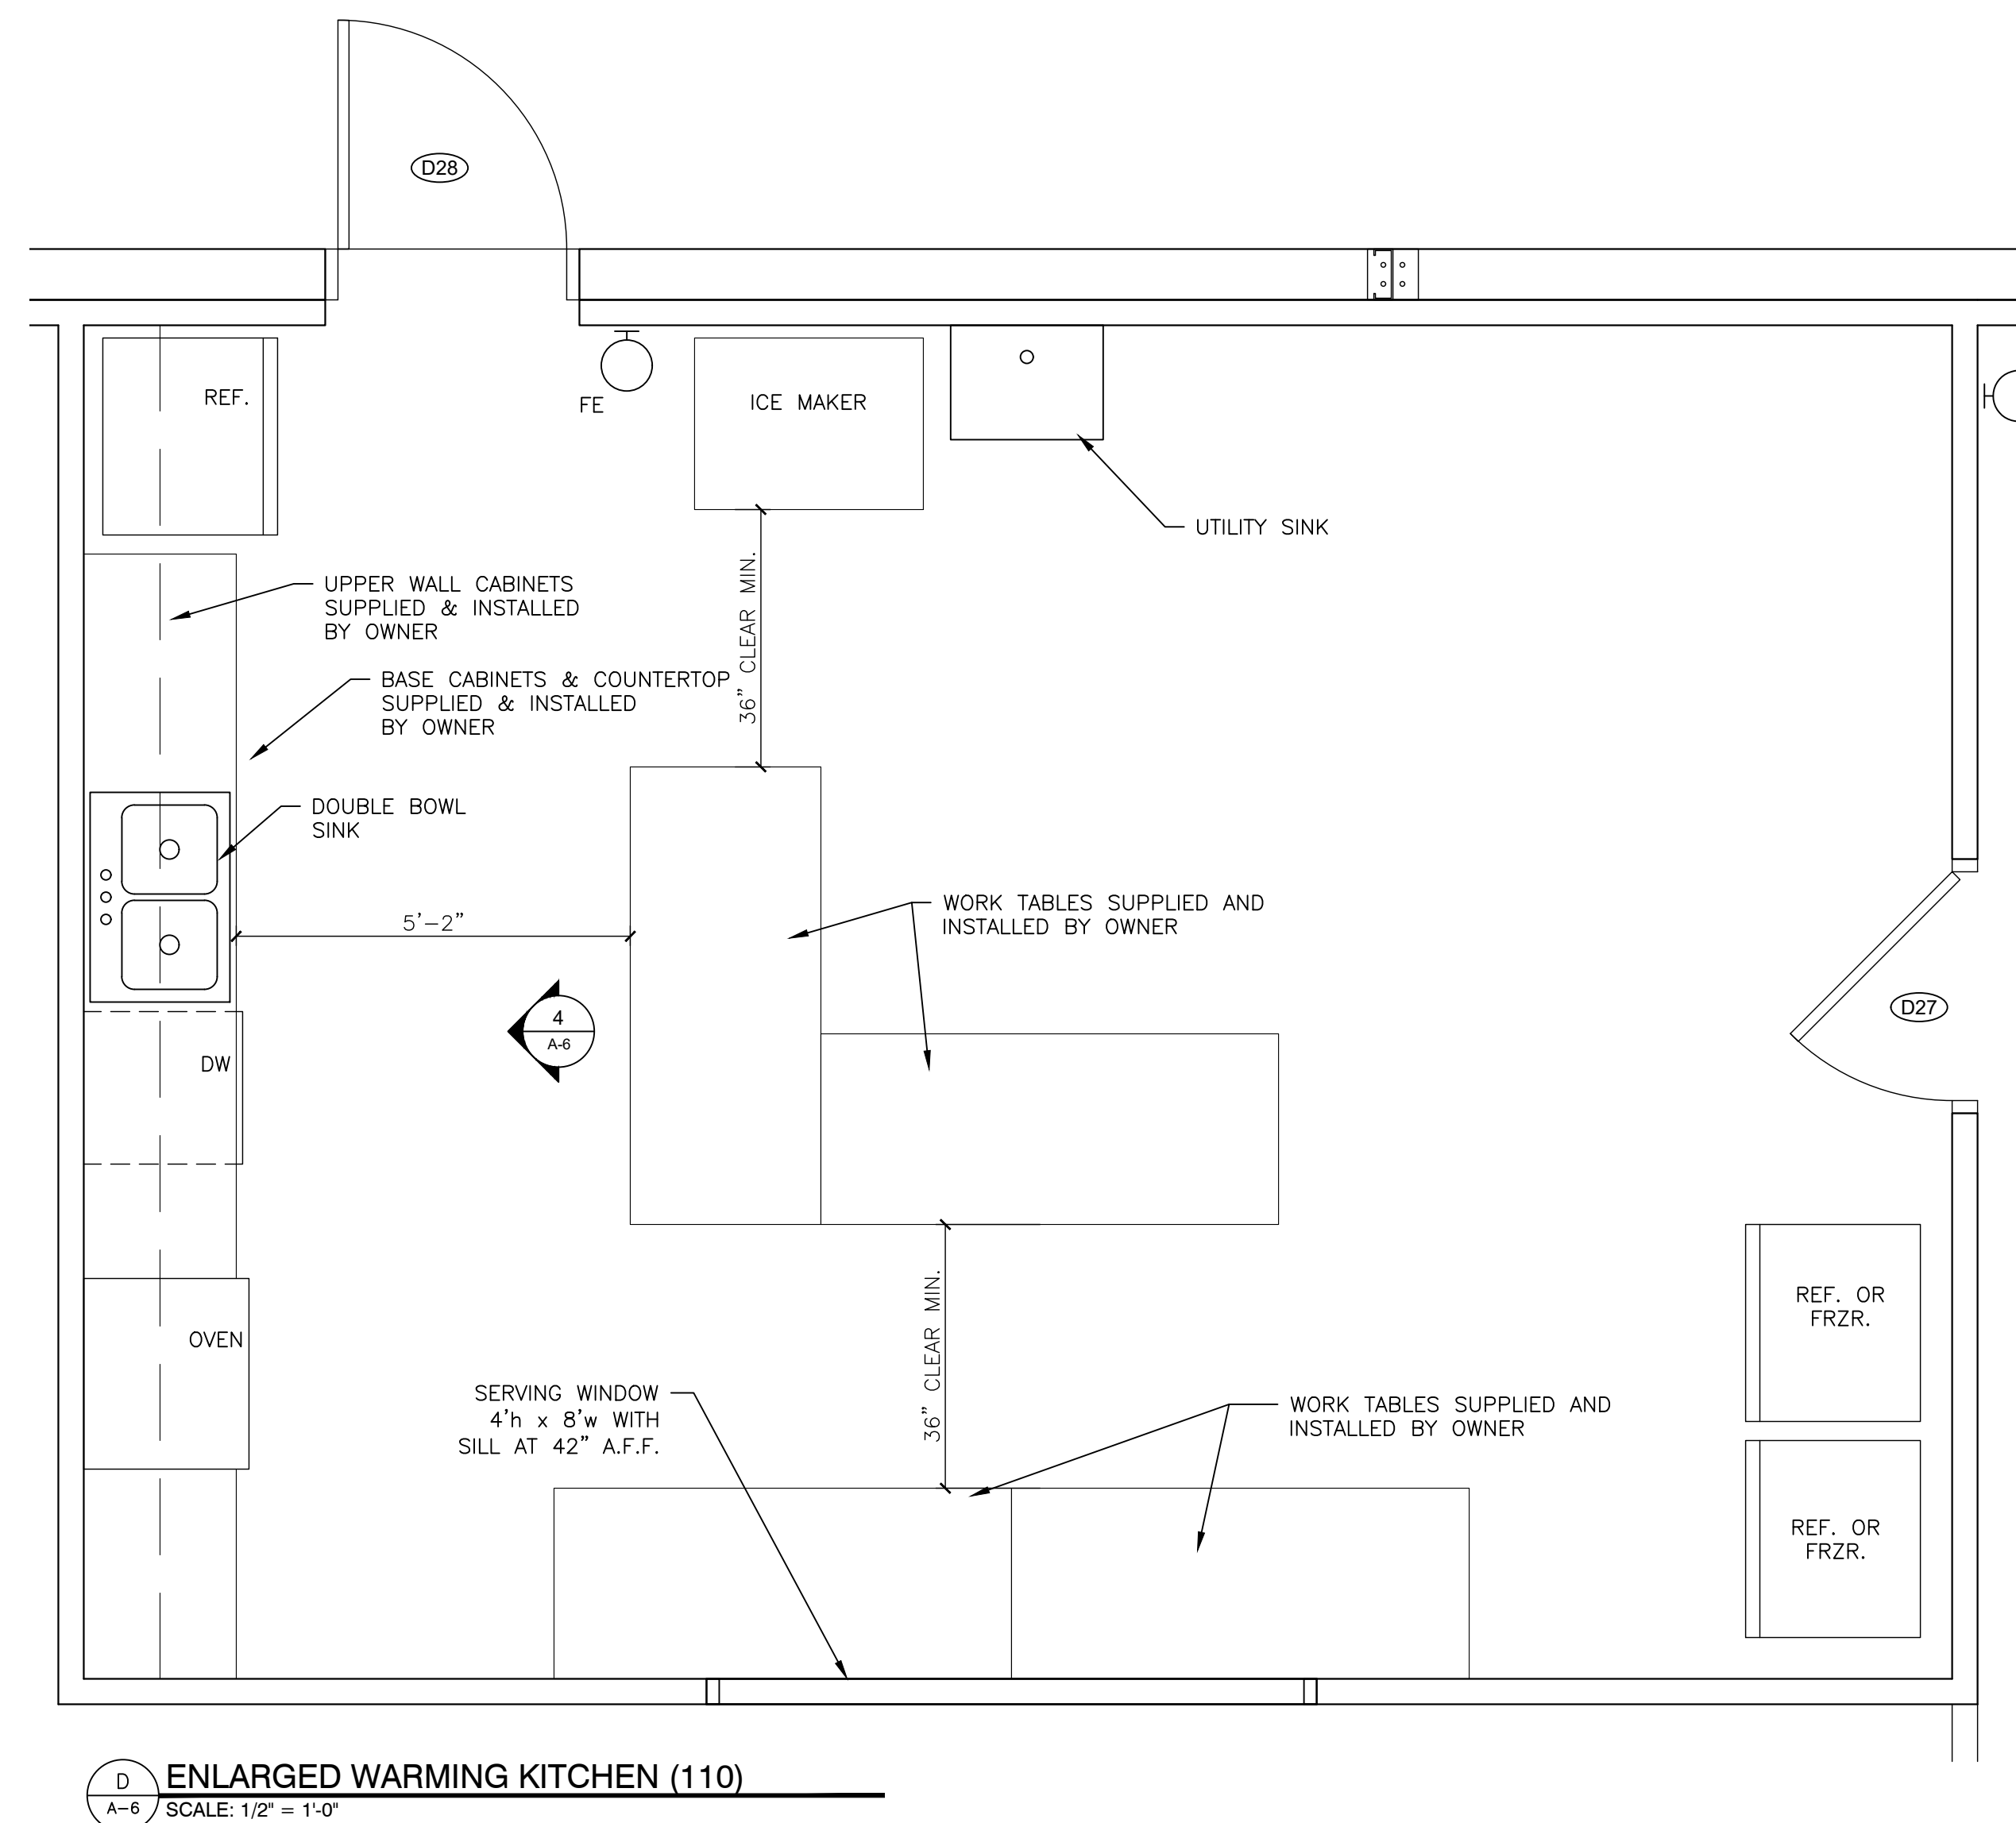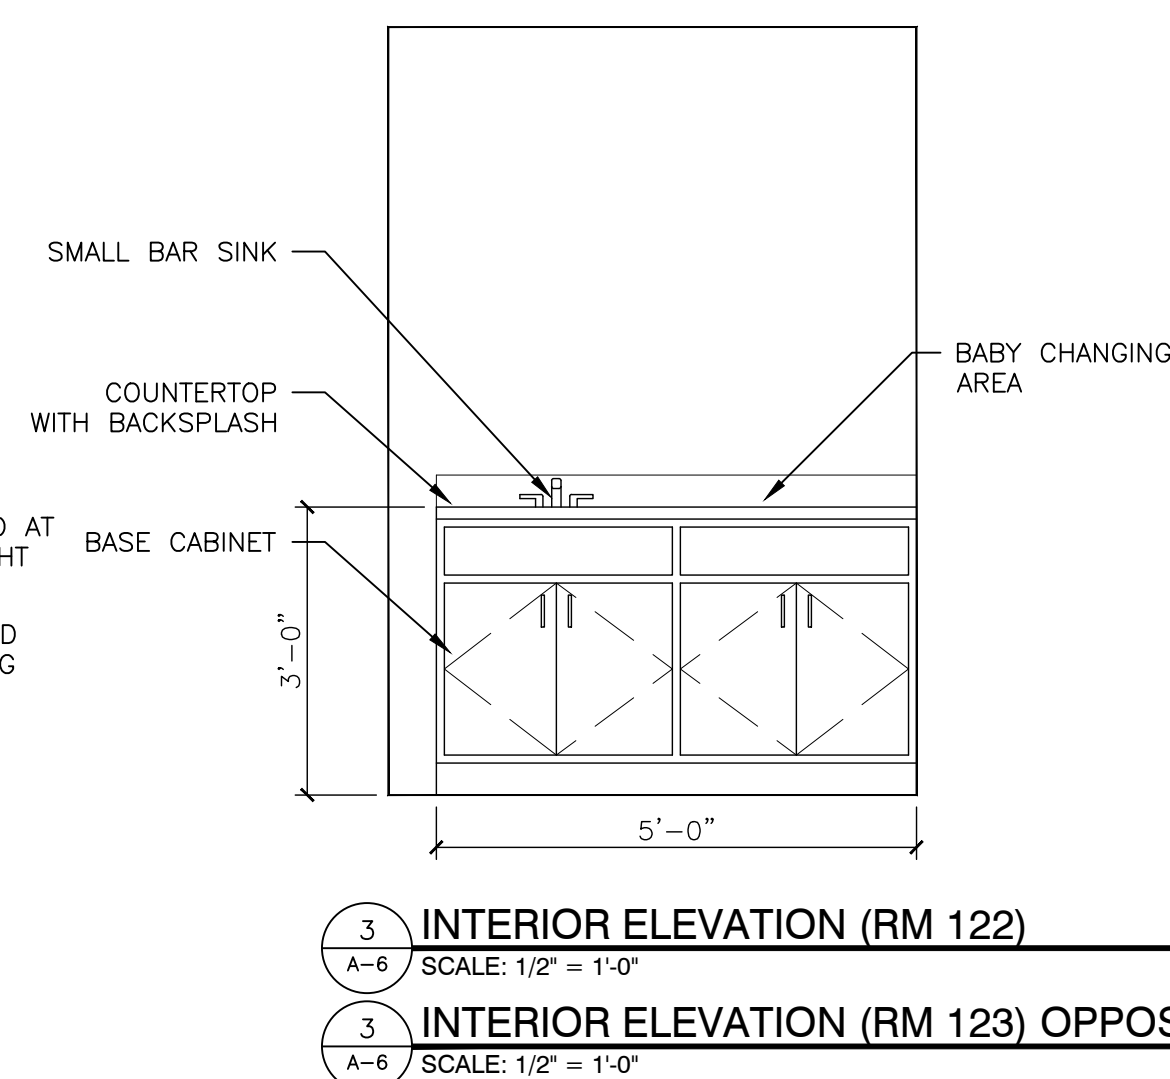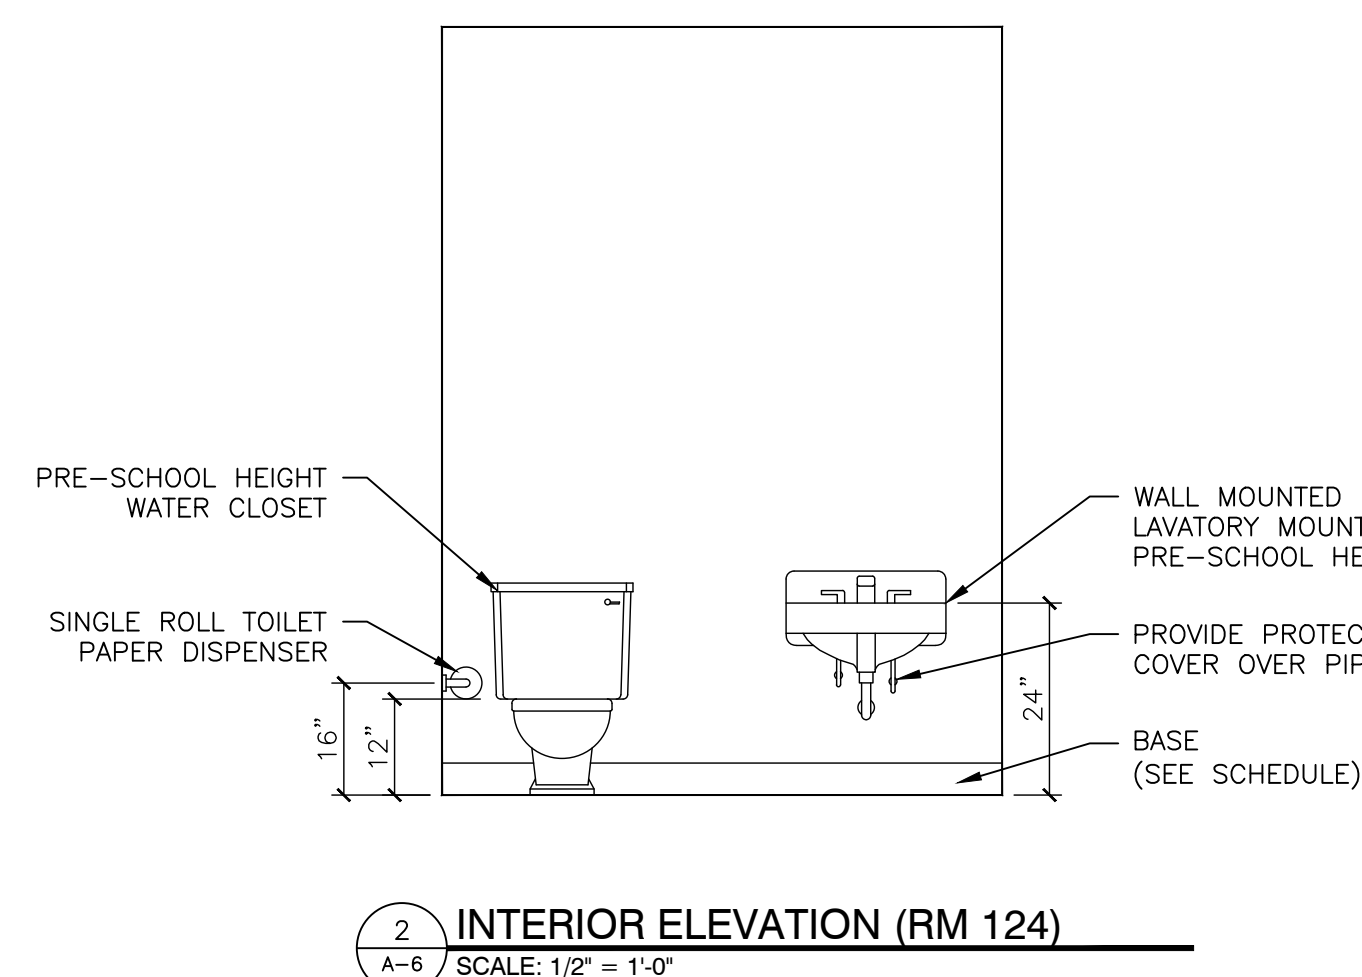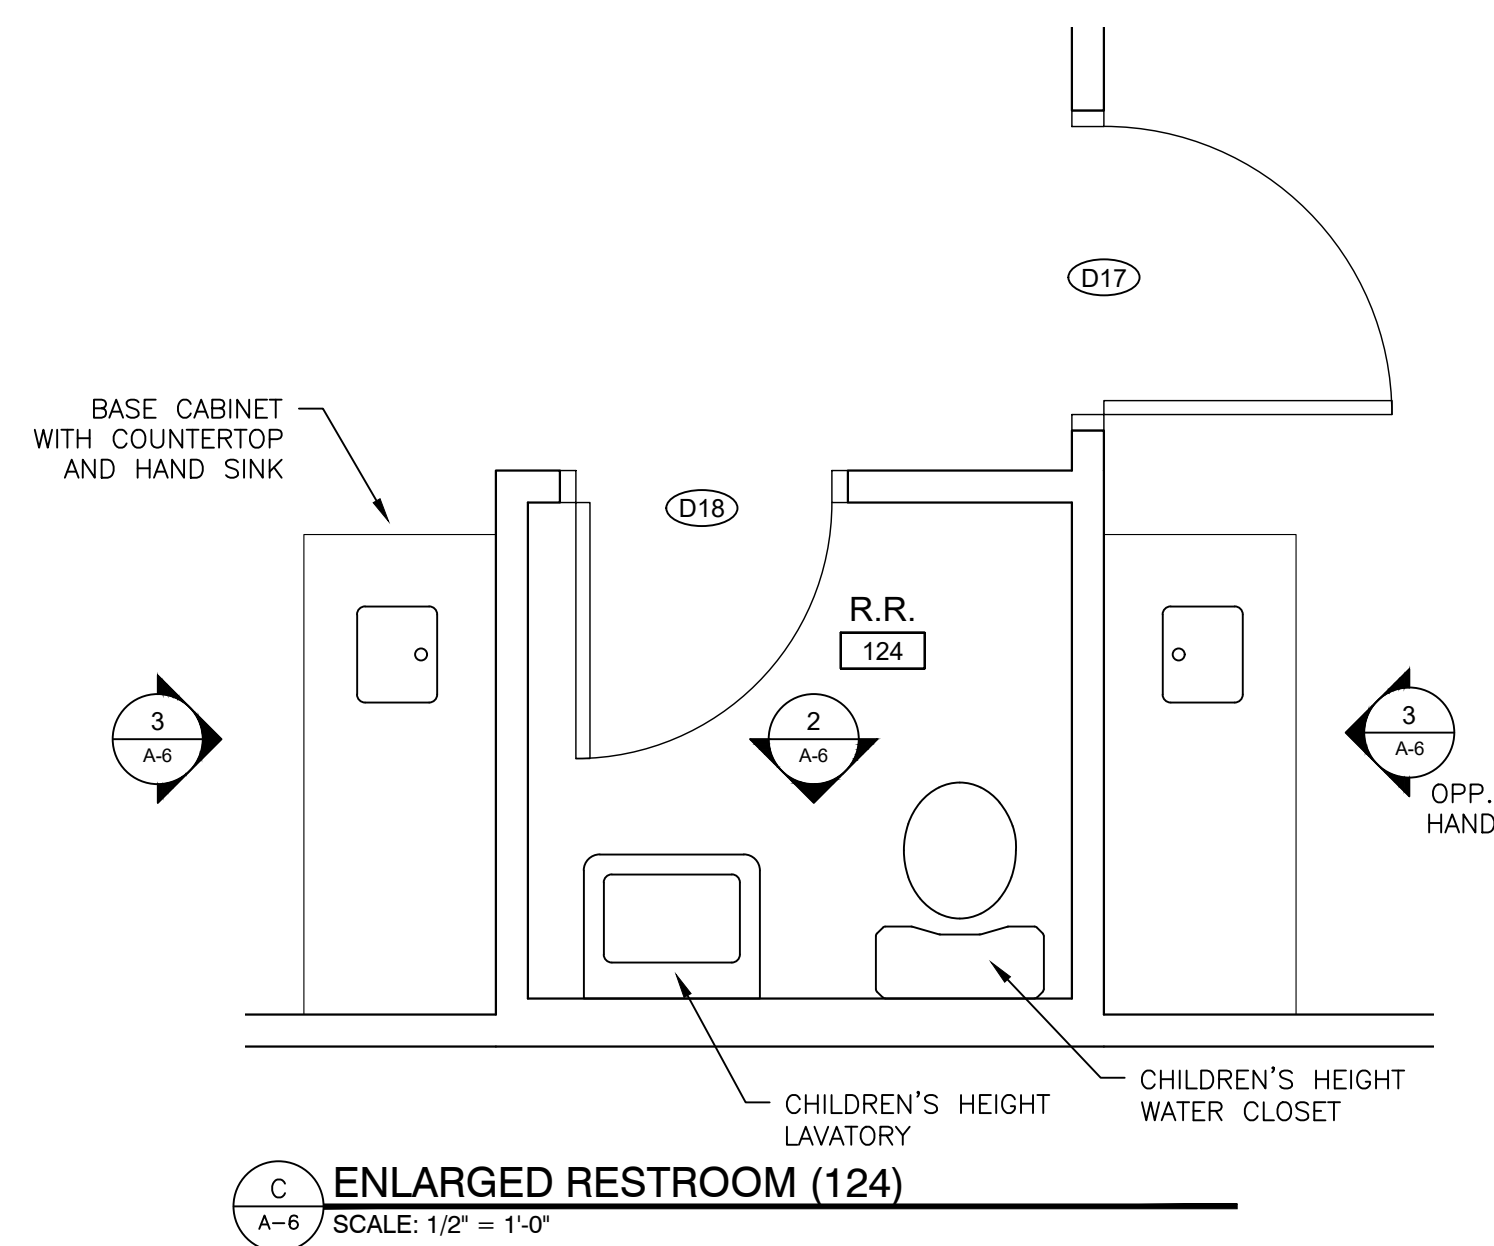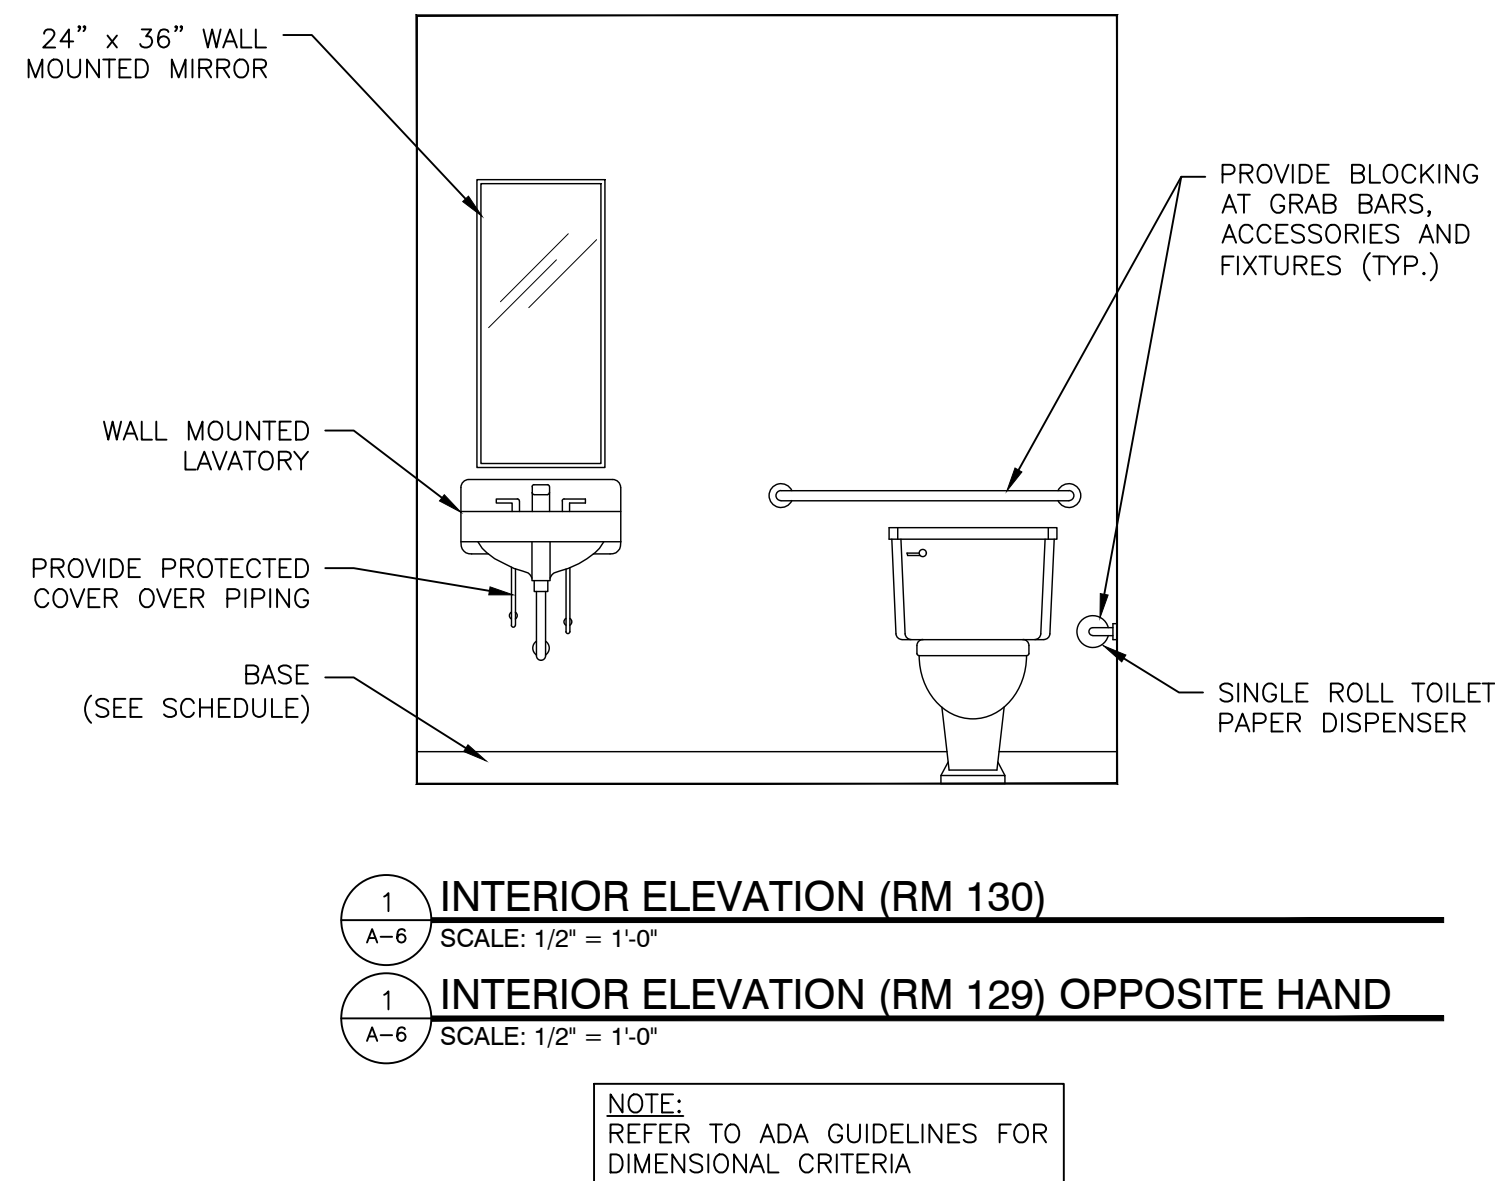A-4
SHEET



[illegible]

SHEET TITLE

ENLARGED PLANS & INTERIOR ELEVATIONS

PROJECT NAME & LOCATION

**SOLID ROCK BAPTIST CHURCH
NEW FACILITY**

U.S. HIGHWAY 278
SOCIAL CIRCLE, GA 30025

SCALE		AS SHOWN
PROJECT NO		C21-0024
BY	KRB	A-6
DATE	2-10-2022	
		SHEET

